


**Проект архитектурных решений
Экопарка «Красивая поляна»**

**Демский район г. Уфа РБ
на берегу озера Красивая поляна**

Ведомость чертежей	
Лист	Наименование
1	Титульный лист
2	Общие данные
3	Ситуационный план
4	План ресторана
5	Фасад - 1
6	Фасад - 2
7	Фасад - 3
8	Фасад - 4
9	Разрез 1-1, разрез 2-2
10	3D вид ресторана
11	3D вид ресторана
12	3D вид ресторана
13	3D вид ресторана
14	3D вид ресторана
15	3D вид ресторана


Ведомость чертежей	
16	3D вид ресторана
17	3D вид ресторана
18	3D вид ресторана
19	3D вид ресторана
20	План беседки с мангалом
21	Фасады беседки
22	Разрез 3-3, разрез 4-4
23	3D вид беседки
24	3D вид беседки
25	3D вид беседки
26	3D вид беседки
27	План лобного места
28	3D вид лобного места
29	3D вид лобного места
30	Спецификация

						АР - 1		
						Проект архитектурных решений Экопарк «Красивая поляна» в Демском районе г. Уфа РБ на берегу озера Красивая поляна		
Изм.	Кол.уч.	Лист	№Док.	Подп.	Дата		Стадия	Лист
Разработал		Закиров			04.2025		АР-1	2
Проверил		Закиров			04.2025	Общие данные		
Норм. контроль		Закиров			04.2025			

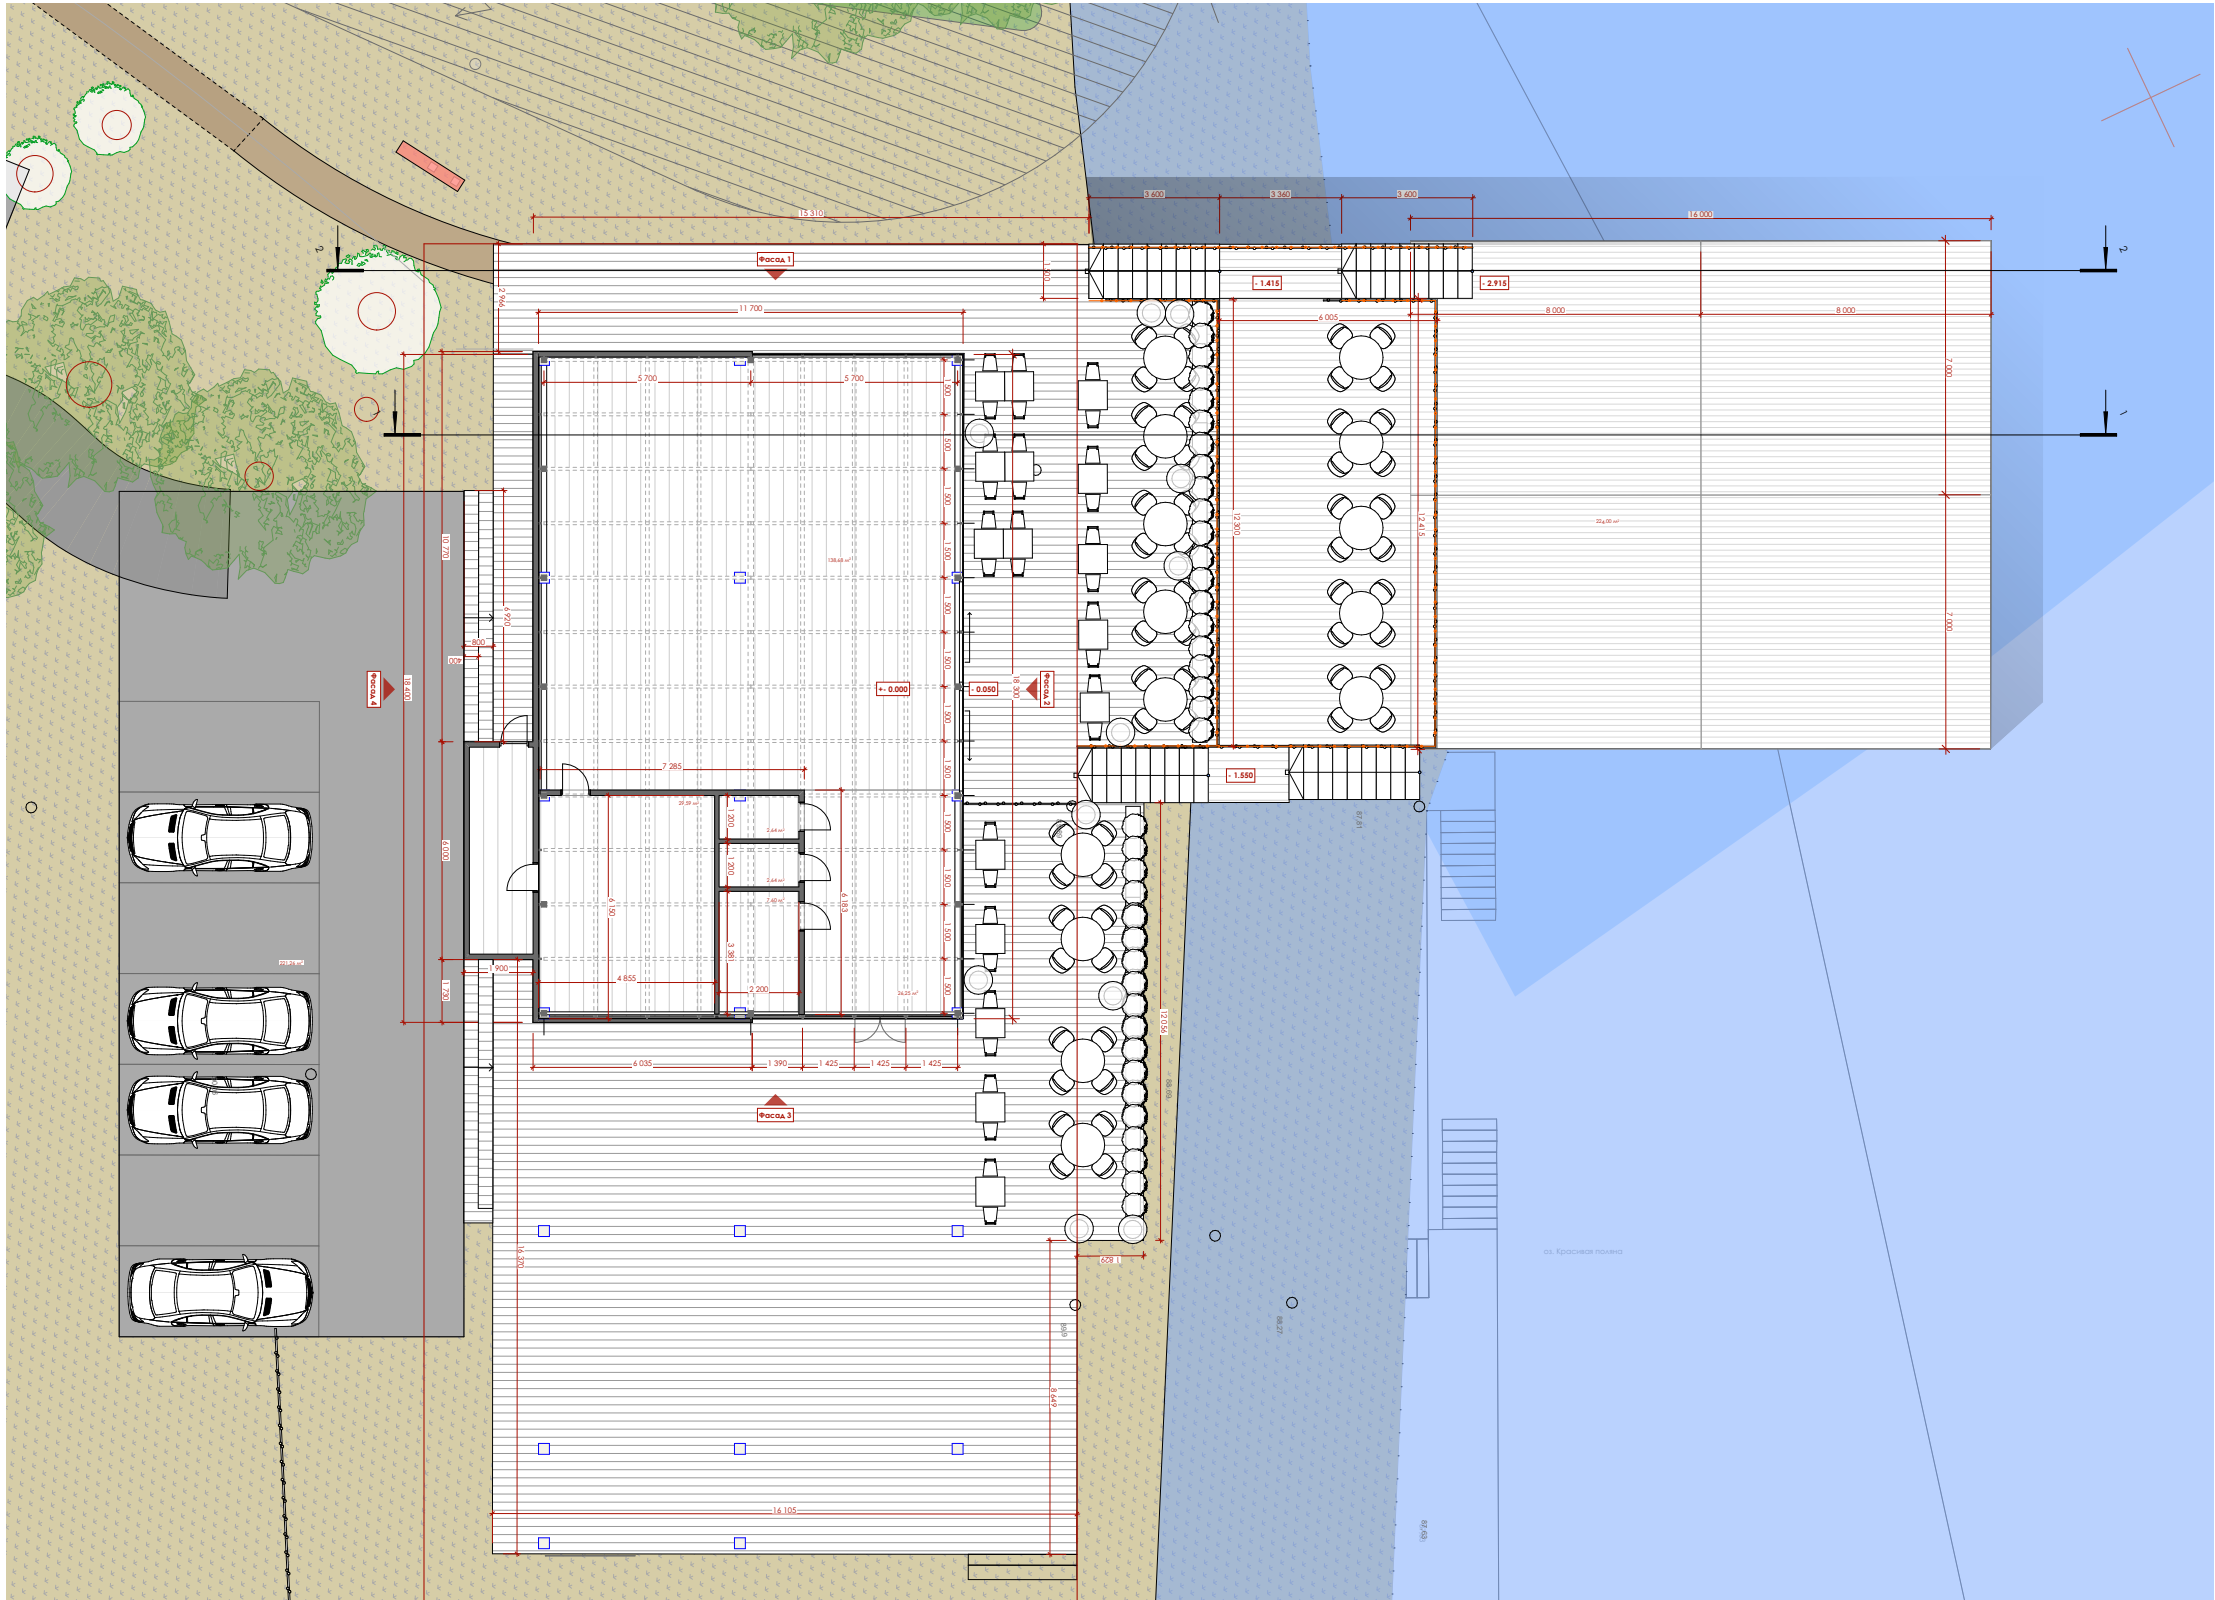


- Примечания:
- 1. За 0.000 принять уровень пола ресторана.
 - 2. Конструктивные узлы, толщины утеплителя, размеры конструкций определить со специалистами.
 - 3. Количество и расположение вентиляционных каналов/дымохода определить со специалистами.
 - 4. Вент. каналы/дымоход выполнить герметично и вывести на необходимую высоту предварительно проконсультировавшись со специалистами.
 - 5. Конструктивные узлы, толщины утеплителя, размеры конструкций определить со специалистами.
 - 6. Для строительства террасы вокруг рекомендуется использовать металлические сваи в качестве основы конструкции.
 - 7. Рамы окон выполнить в цвете RAL 7024/7022, перед заказом снять замеры, согласовать с авторами проекта.
 - 8. Данные чертежи не носят технический характер и не являются строительными.

						АР - 1			
						Проект архитектурных решений Экопарка «Красивая поляна» в Демском районе г. Уфа РБ на берегу озера Красивая поляна			
Изм.	Кол.уч.	Лист	№Док.	Подп.	Дата		Стадия	Лист	Листов
Разработал		Закиров			04.2025		АР-1	4	
Проверил		Закиров			04.2025	План ресторана			
Норм. контроль		Закиров			04.2025				

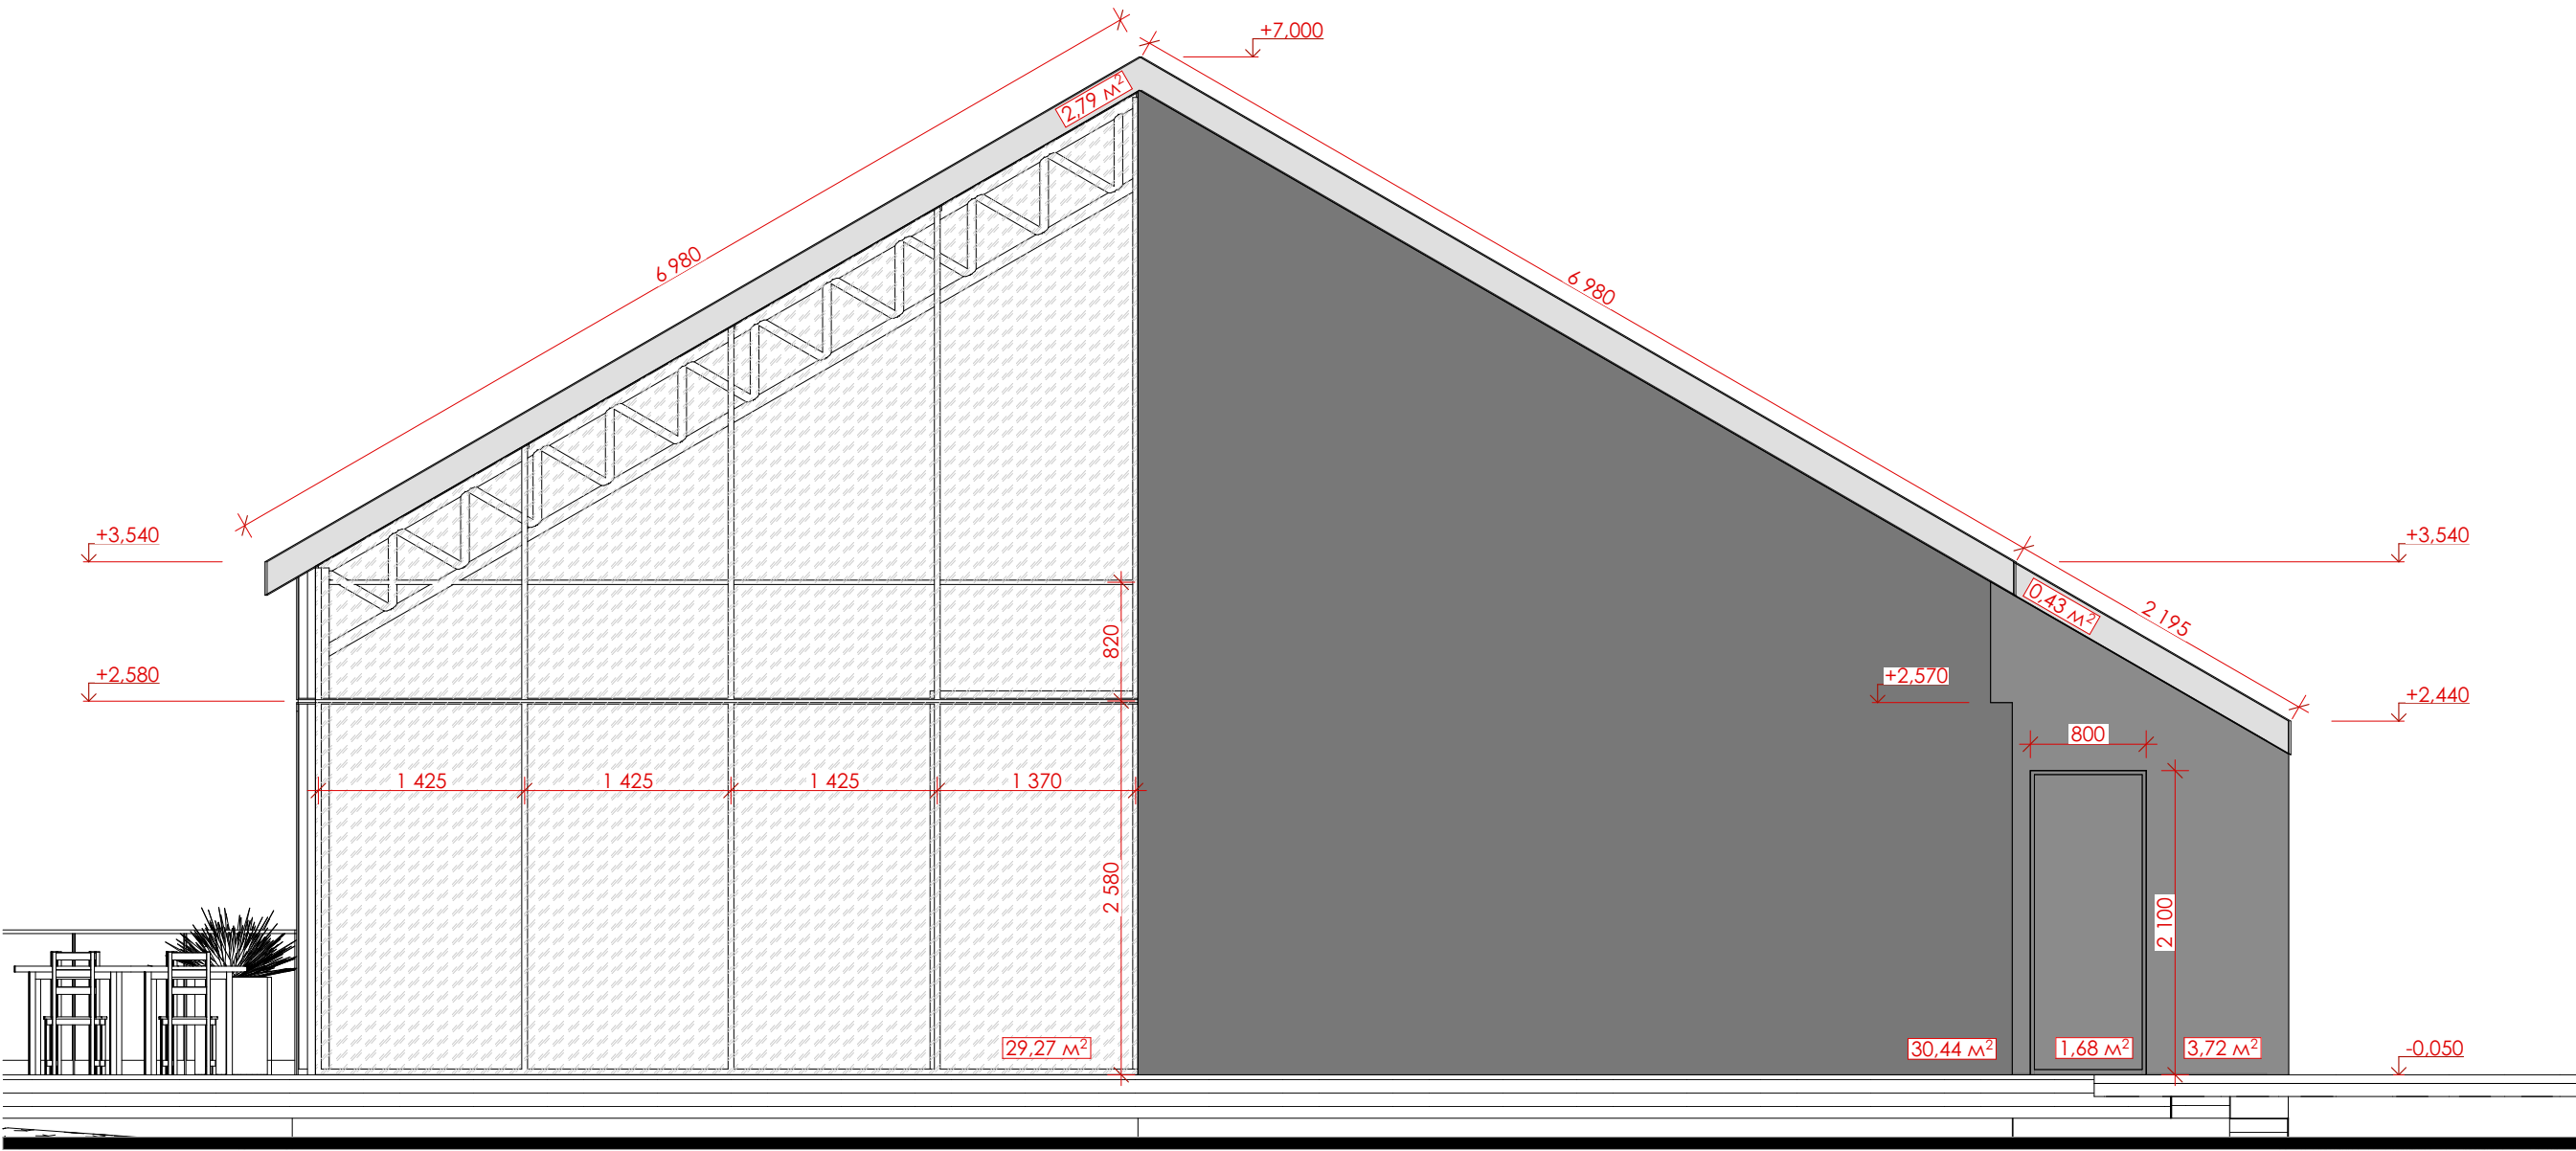


Примечания:
1. За 0,000 принять уровень пола ресторана.
2. Конструктивные узлы, толщины утеплителя, размеры конструкций определить со специалистами (конструкторами, строителями).
3. Количество вентиляционных каналов определить со специалистами.
4. Вент. каналы/дымоход выполнить герметично и вывести на необходимую высоту предварительно проконсультировавшись со специалистами.
5. Вент. каналы/дымоход утеплить, материал обшивки - проф. лист в цвет кровли.
6. Рамы окон выполнить в цвете RAL 7024/7022, перед заказом снять замеры, согласовать с авторами проекта.
7. Данные чертежи не носят технический характер и не являются строительными

						АР - 1			
						Проект архитектурных решений Экопарка «Красивая поляна» в Демском районе г. Уфа РБ на берегу озера Красивая поляна			
Изм.	Кол.уч.	Лист	№Док.	Подп.	Дата		Стадия	Лист	Листов
Разработал	Закиров				04.2025		АР-1	5	
Проверил	Закиров				04.2025	Фасад - 1			
Норм. контроль	Закиров				04.2025				

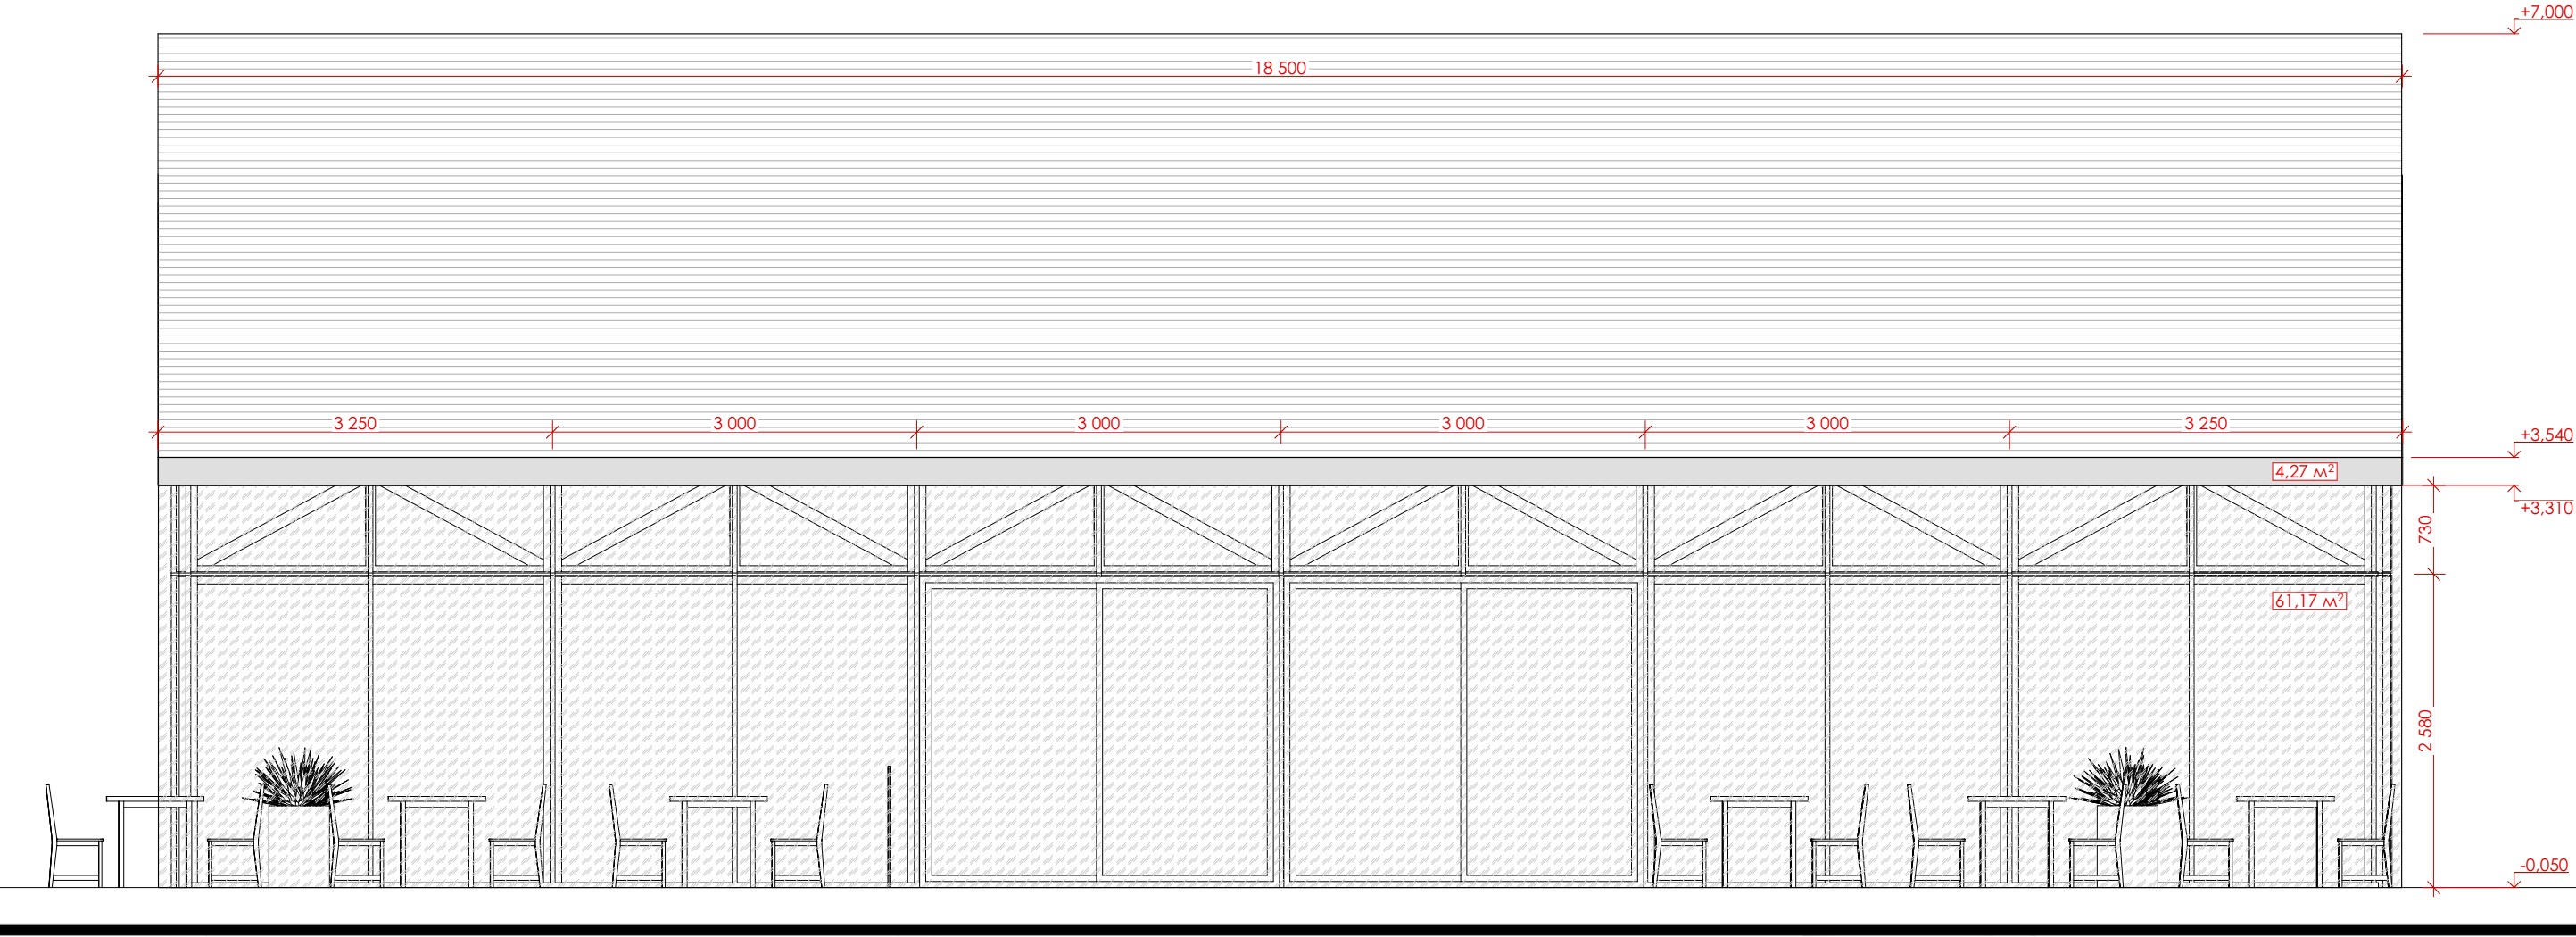


Примечания:
1. За 0,000 принять уровень пола ресторана.
2. Конструктивные узлы, толщины утеплителя, размеры конструкций определить со специалистами (конструктрами, строителями).
3. Количество вентиляционных каналов определить со специалистами.
4. Вент. каналы/дымоход выполнить герметично и вывести на необходимую высоту предварительно проконсультировавшись со специалистами.
5. Вент. каналы/дымоход утеплить, материал обшивки - проф. лист в цвет кровли.
6. Рамы окон выполнить в цвете RAL 7024/7022, перед заказом снять замеры, согласовать с авторами проекта.
7. Данные чертежи не носят технический характер и не являются строительными

						АР - 1			
						Проект архитектурных решений Экопарка «Красивая поляна» в Демском районе г. Уфа РБ на берегу озера Красивая поляна			
Изм.	Кол.уч.	Лист	№Док.	Подп.	Дата		Стадия	Лист	Листов
Разработал		Закиров			04.2025		АР-1	6	
Проверил		Закиров			04.2025	Фасад - 2			
Норм. контроль		Закиров			04.2025				

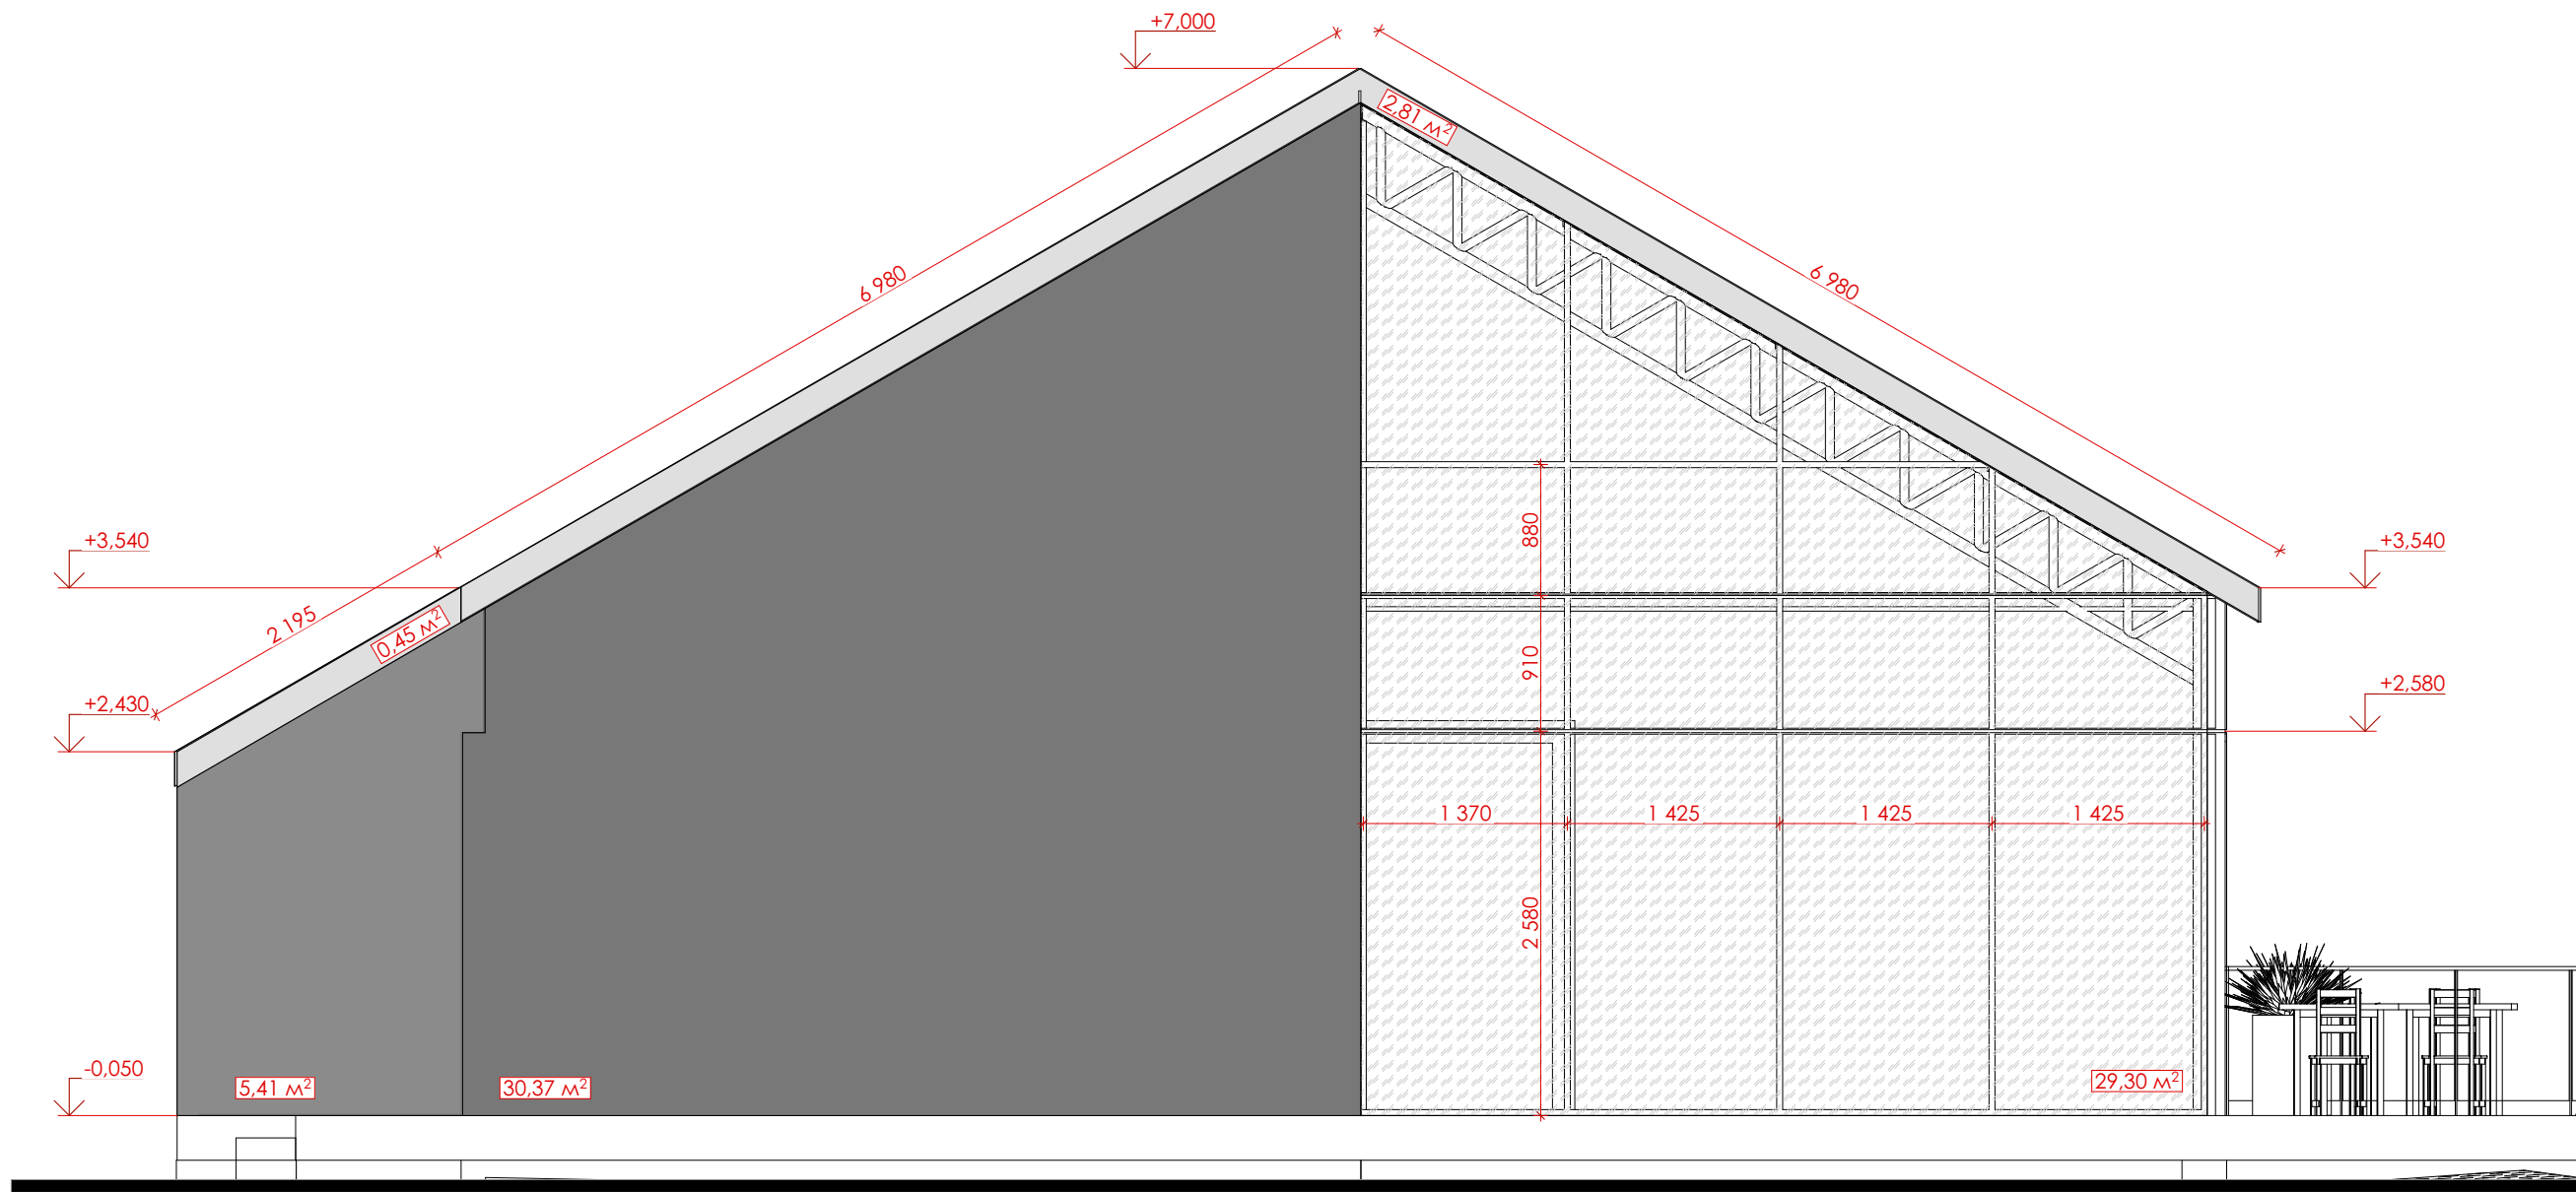


Примечания:
1. За 0,000 принять уровень пола ресторана.
2. Конструктивные узлы, толщины утеплителя, размеры конструкций определить со специалистами (конструктрами, строителями).
3. Количество вентиляционных каналов определить со специалистами.
4. Вент. каналы/дымоход выполнить герметично и вывести на необходимую высоту предварительно проконсультировавшись со специалистами.
5. Вент. каналы/дымоход утеплить, материал обшивки - проф. лист в цвет кровли.
6. Рамы окон выполнить в цвете RAL 7024/7022, перед заказом снять замеры, согласовать с авторами проекта.
7. Данные чертежи не носят технический характер и не являются строительными

						АР - 1			
						Проект архитектурных решений Экопарка «Красивая поляна» в Демском районе г. Уфа РБ на берегу озера Красивая поляна			
Изм.	Кол.уч.	Лист	№Док.	Подп.	Дата		Стадия	Лист	Листов
Разработал	Закиров				04.2025		АР-1	7	
Проверил	Закиров				04.2025	Фасад - 3			
Норм. контроль	Закиров				04.2025				

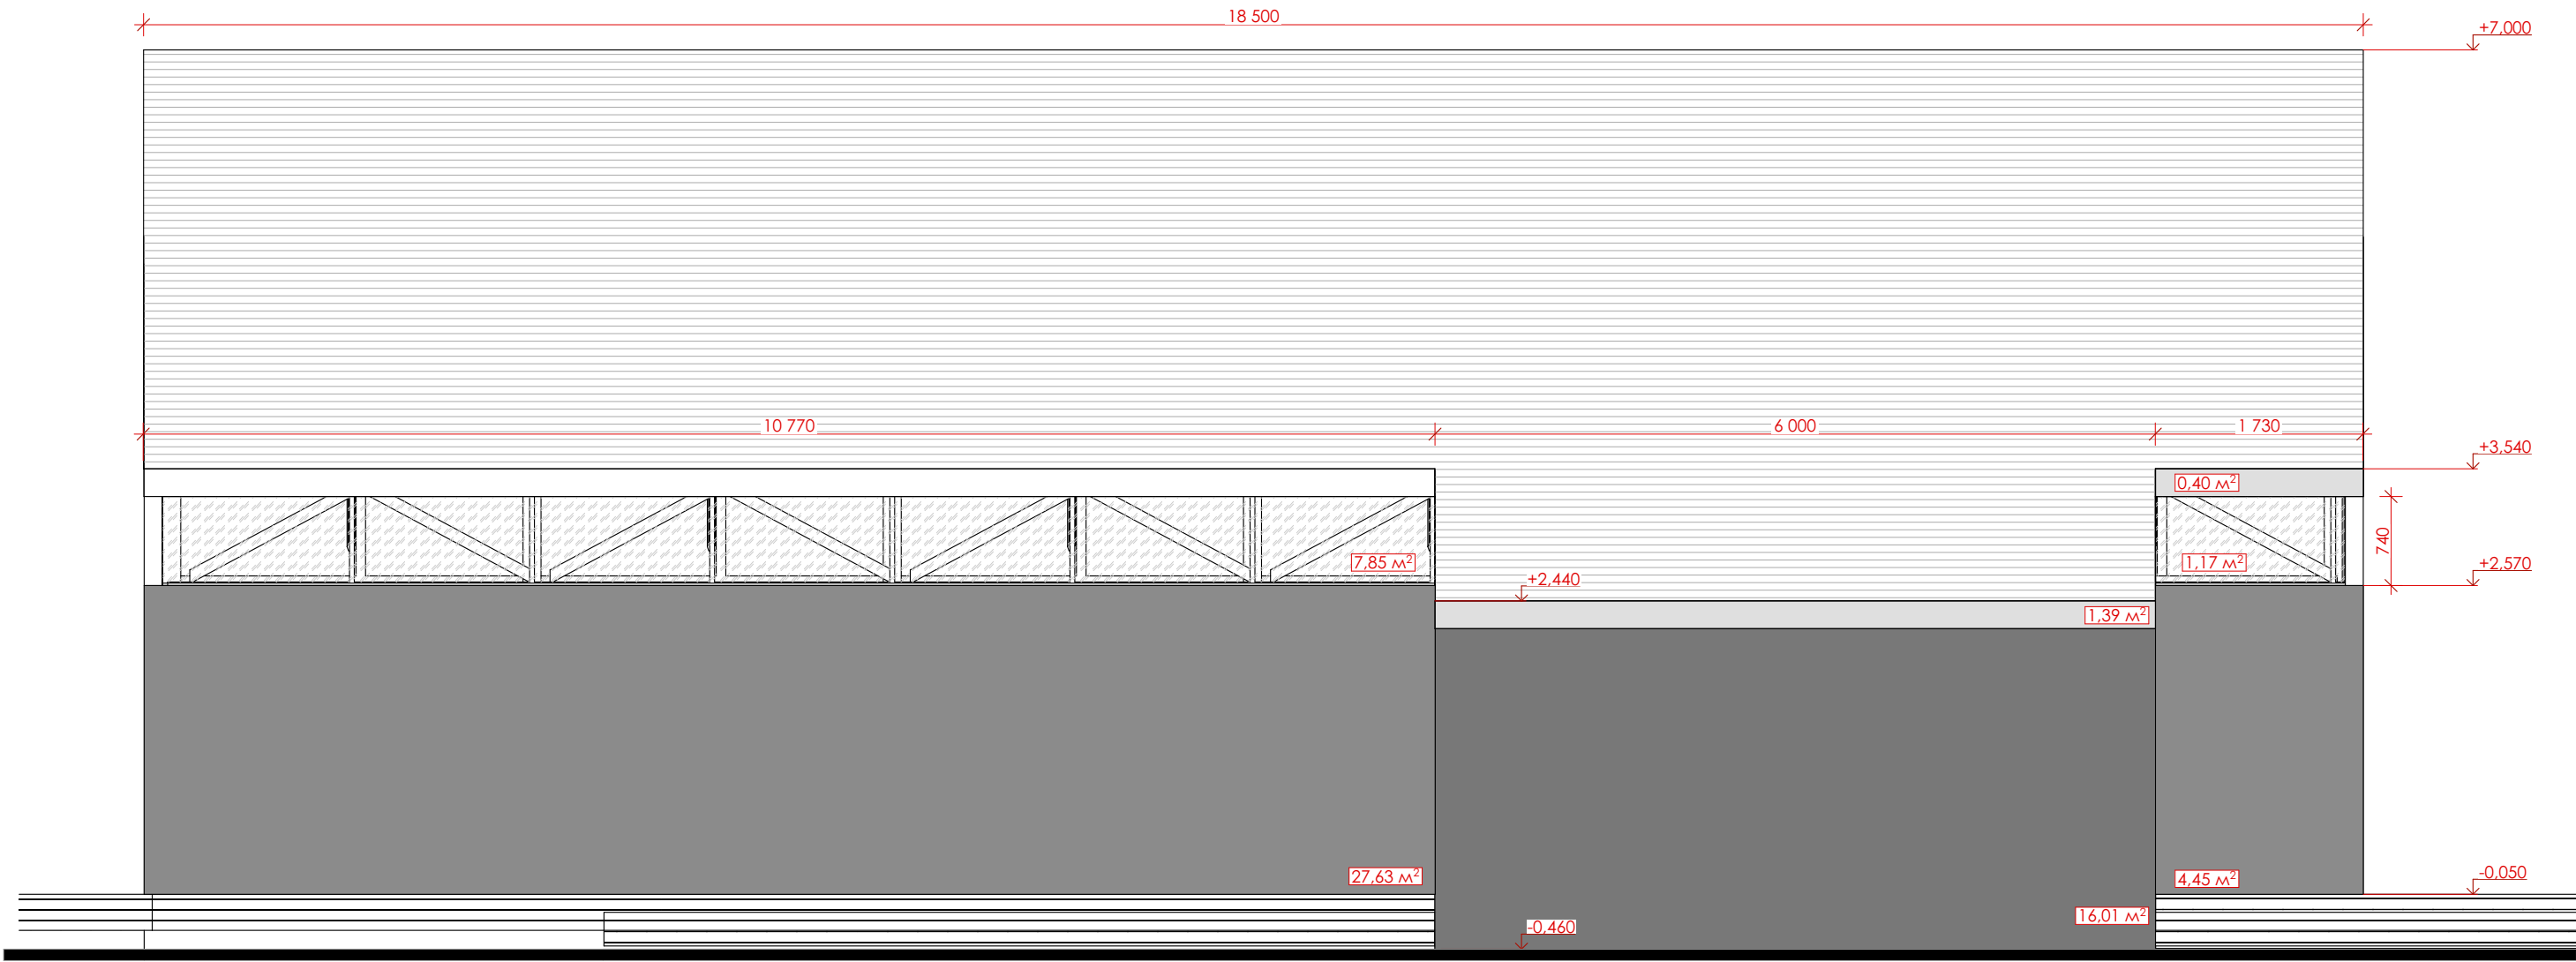


Примечания:
1. За 0,000 принять уровень пола ресторана.
2. Конструктивные узлы, толщины утеплителя, размеры конструкций определить со специалистами (конструктрами, строителями).
3. Количество вентиляционных каналов определить со специалистами.
4. Вент. каналы/дымоход выполнить герметично и вывести на необходимую высоту предварительно проконсультировавшись со специалистами.
5. Вент. каналы/дымоход утеплить, материал обшивки - проф. лист в цвет кровли.
6. Рамы окон выполнить в цвете RAL 7024/7022, перед заказом снять замеры, согласовать с авторами проекта.
7. Данные чертежи не носят технический характер и не являются строительными

						АР - 1			
						Проект архитектурных решений Экопарк «Красивая поляна» в Демском районе г. Уфа РБ на берегу озера Красивая поляна			
Изм.	Кол.уч.	Лист	№Док.	Подп.	Дата		Стадия	Лист	Листов
Разработал	Закиров				04.2025		АР-1	8	
Проверил	Закиров				04.2025	Фасад - 4			
Норм. контроль	Закиров				04.2025				

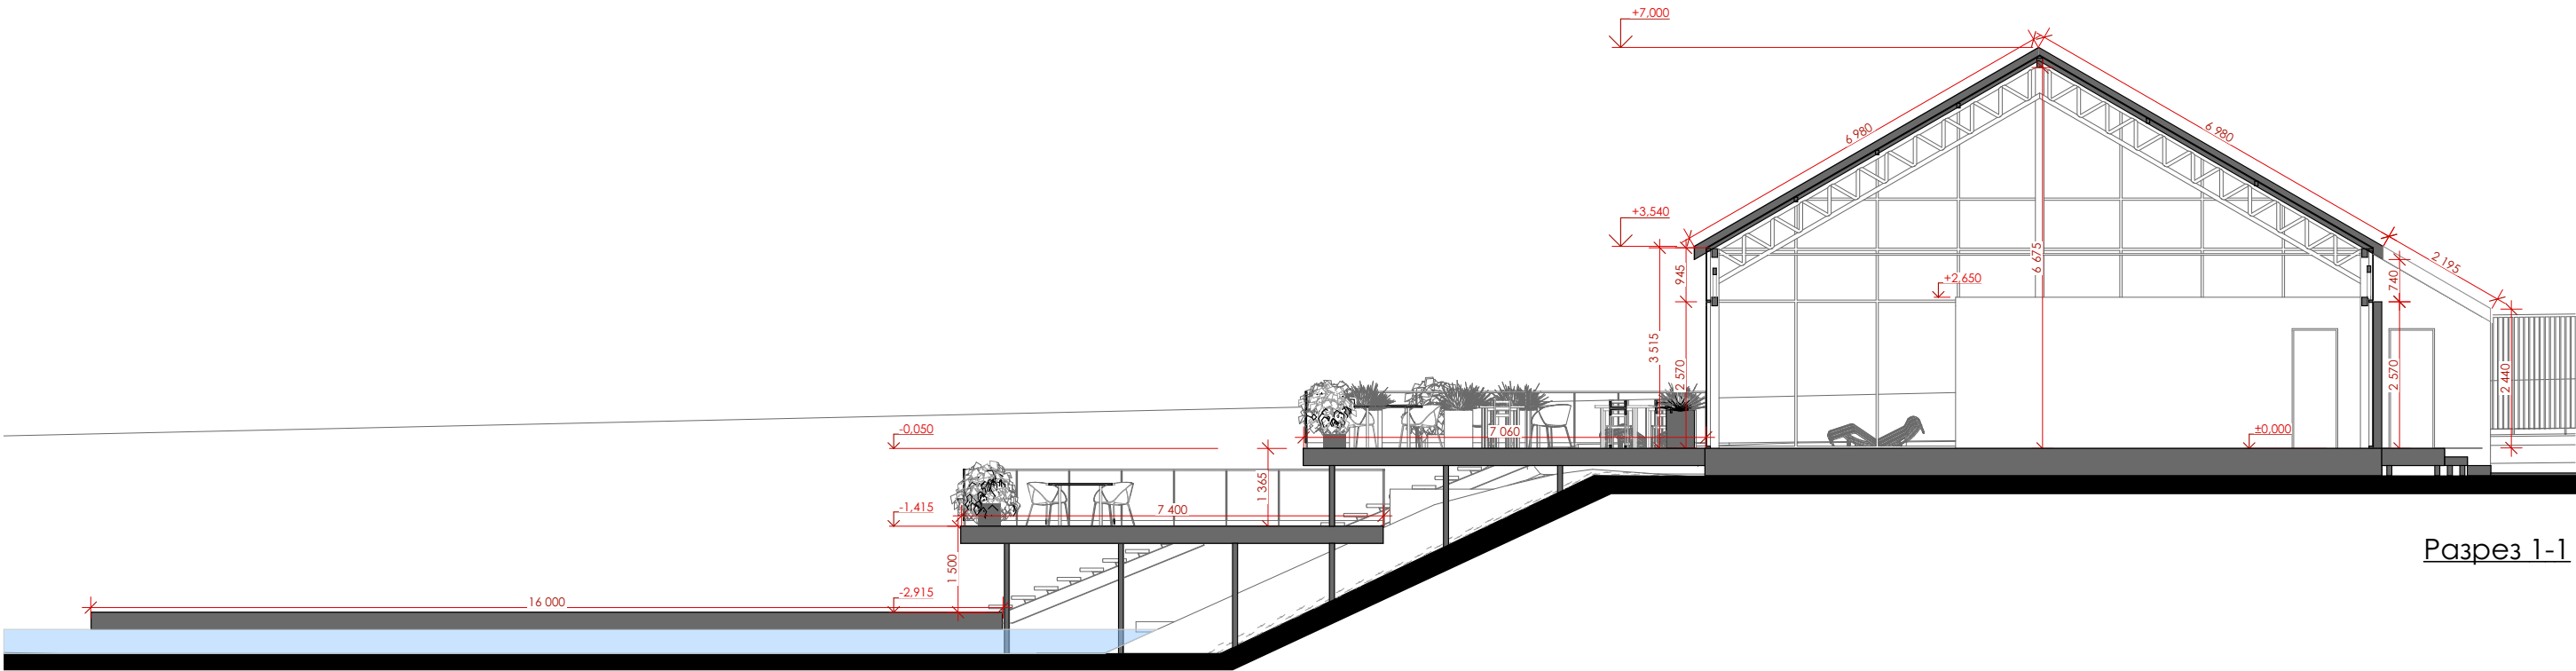


Разрез 1-1

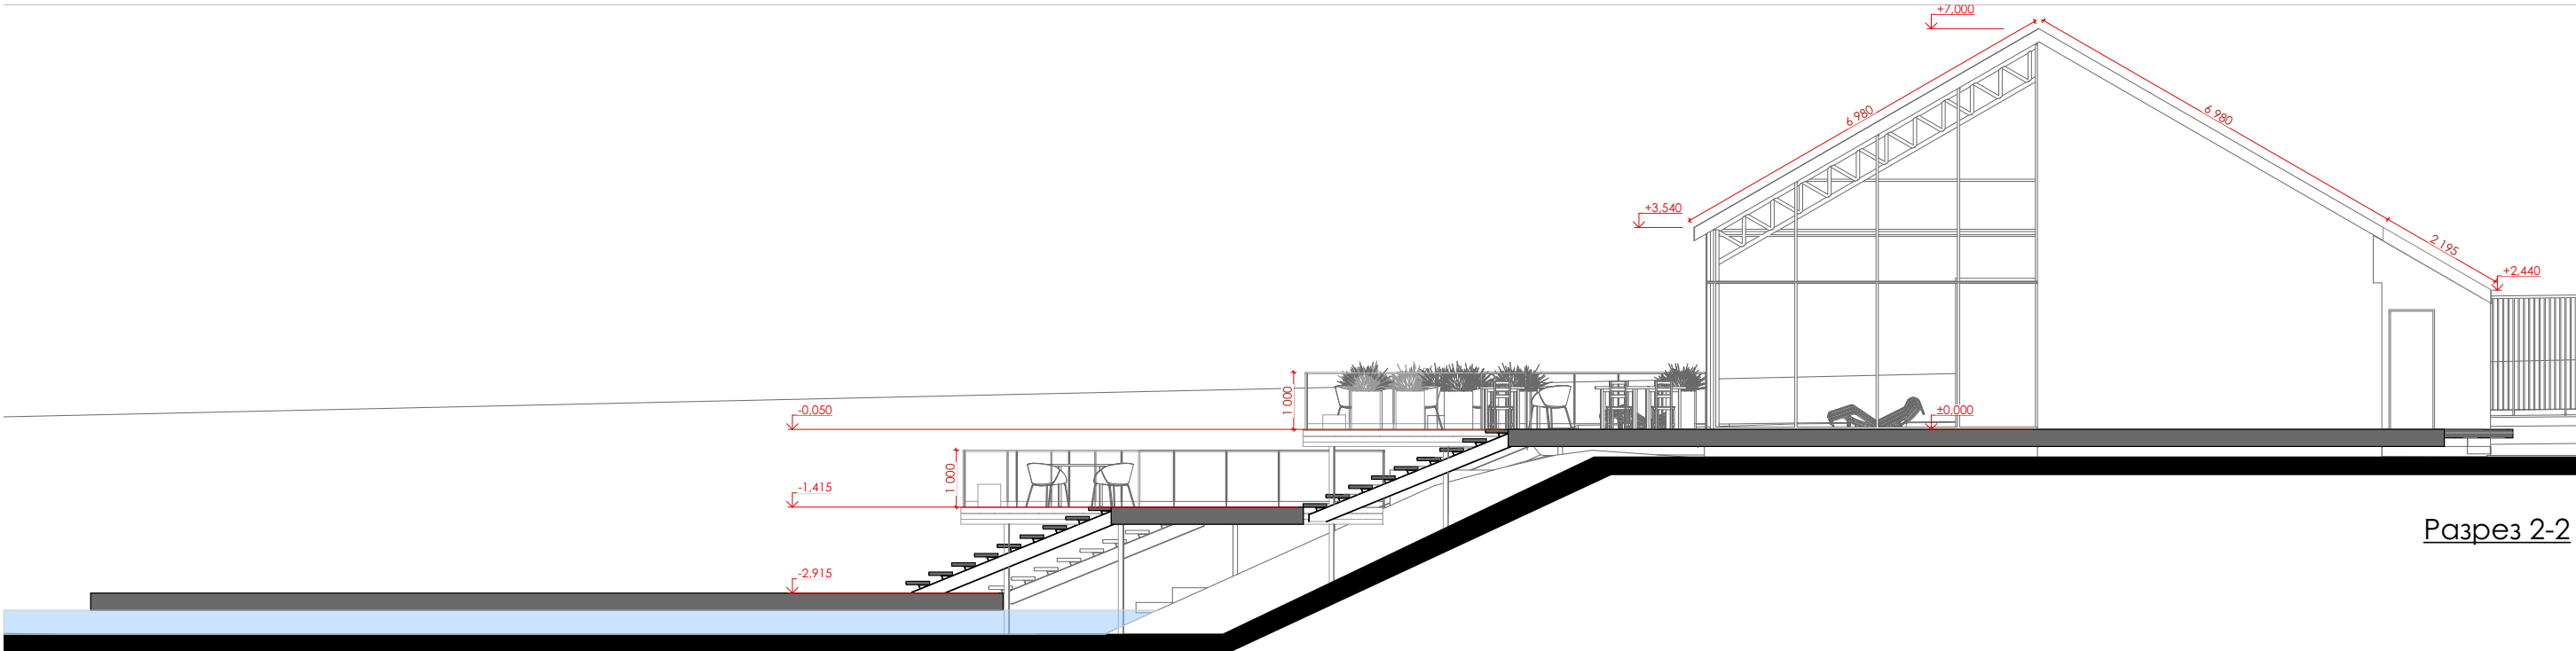


Разрез 2-2

- Примечания:
1. За 0,000 принять уровень пола реторана.
 2. Конструктивные узлы, толщины утеплителя, размеры конструкций определить со специалистами (конструктрами, строителями).
 3. Вент. каналы выполнить герметично и вывести на необходимую высоту предварительно проконсультировавшись со специалистами.
 4. Конструкцию кровли определить со специалистами.
 5. Выполняя отмостку следует предусмотреть минимальный уклон от стен здания.
 6. Предусмотреть ливневую систему водостока.
 7. Размещение, материалы и габариты крылец/порогов определить по месту.
 8. Данные чертежи не носят технический характер и не являются строительными.


						АР - 1			
						Проект архитектурных решений Экопарка «Красивая поляна» в Демском районе г. Уфа РБ на берегу озера Красивая поляна			
Изм.	Кол.уч.	Лист	№Док.	Подп.	Дата		Стадия	Лист	Листов
Разработал		Закиров			04.2025		АР-1	9	
						Разрез 1-1, разрез 2-2			
Проверил		Закиров			04.2025				
Норм. контроль		Закиров			04.2025				

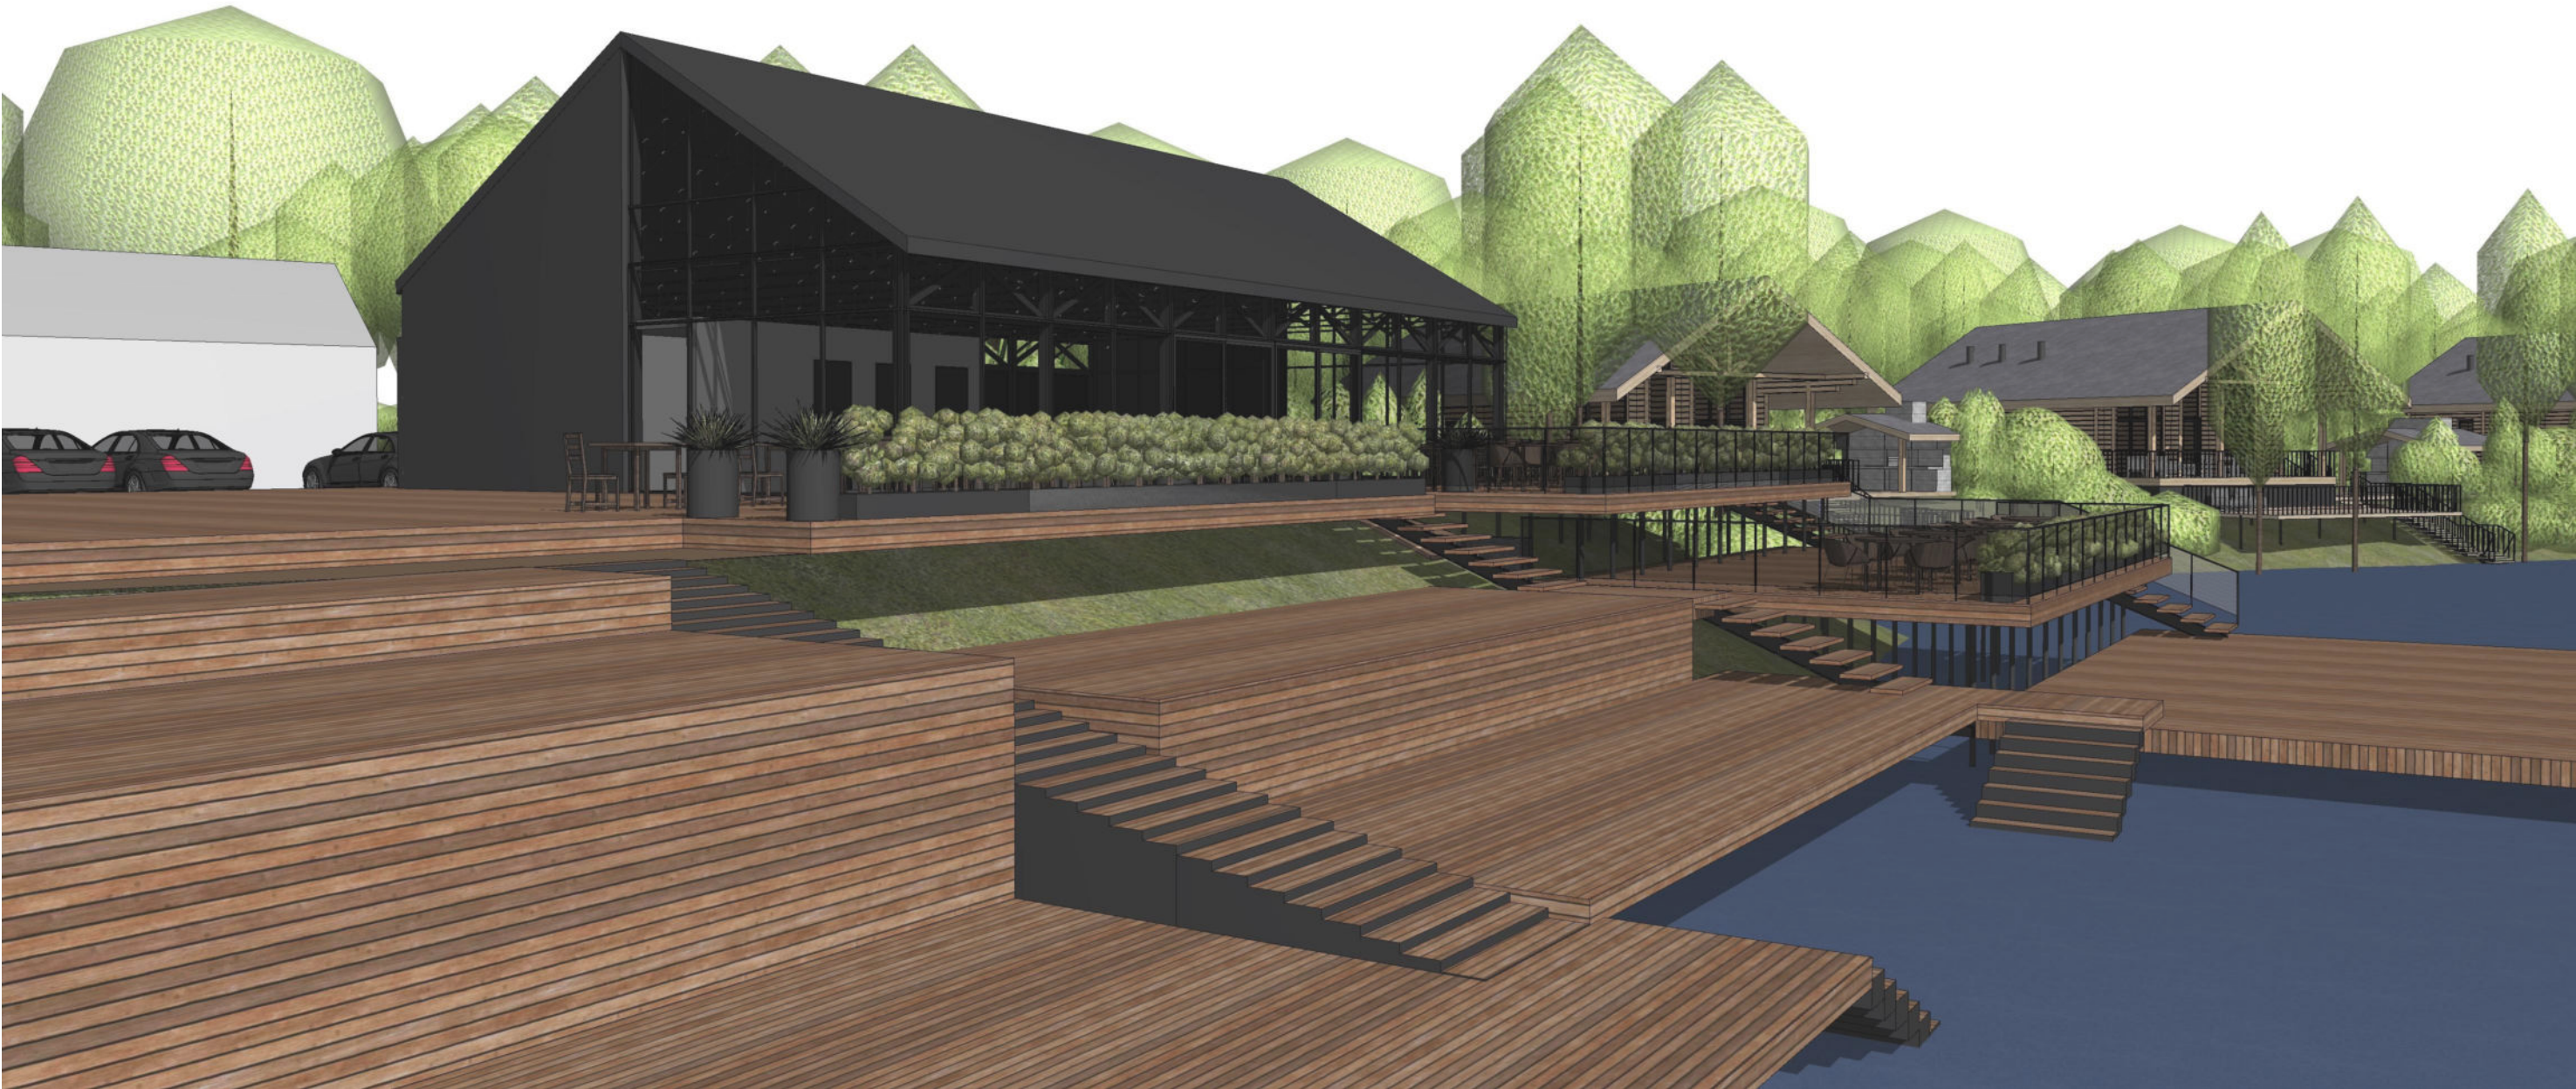


						АР - 1			
						Проект архитектурных решений Экопарка «Красивая поляна» в Демском районе г. Уфа РБ на берегу озера Красивая поляна			
Изм.	Кол.уч.	Лист	№Док.	Подп.	Дата		Стадия	Лист	Листов
Разработал		Закиров			04.2025		АР-1	10	
Проверил		Закиров			04.2025	3D вид ресторана			
Норм. контроль		Закиров			04.2025				

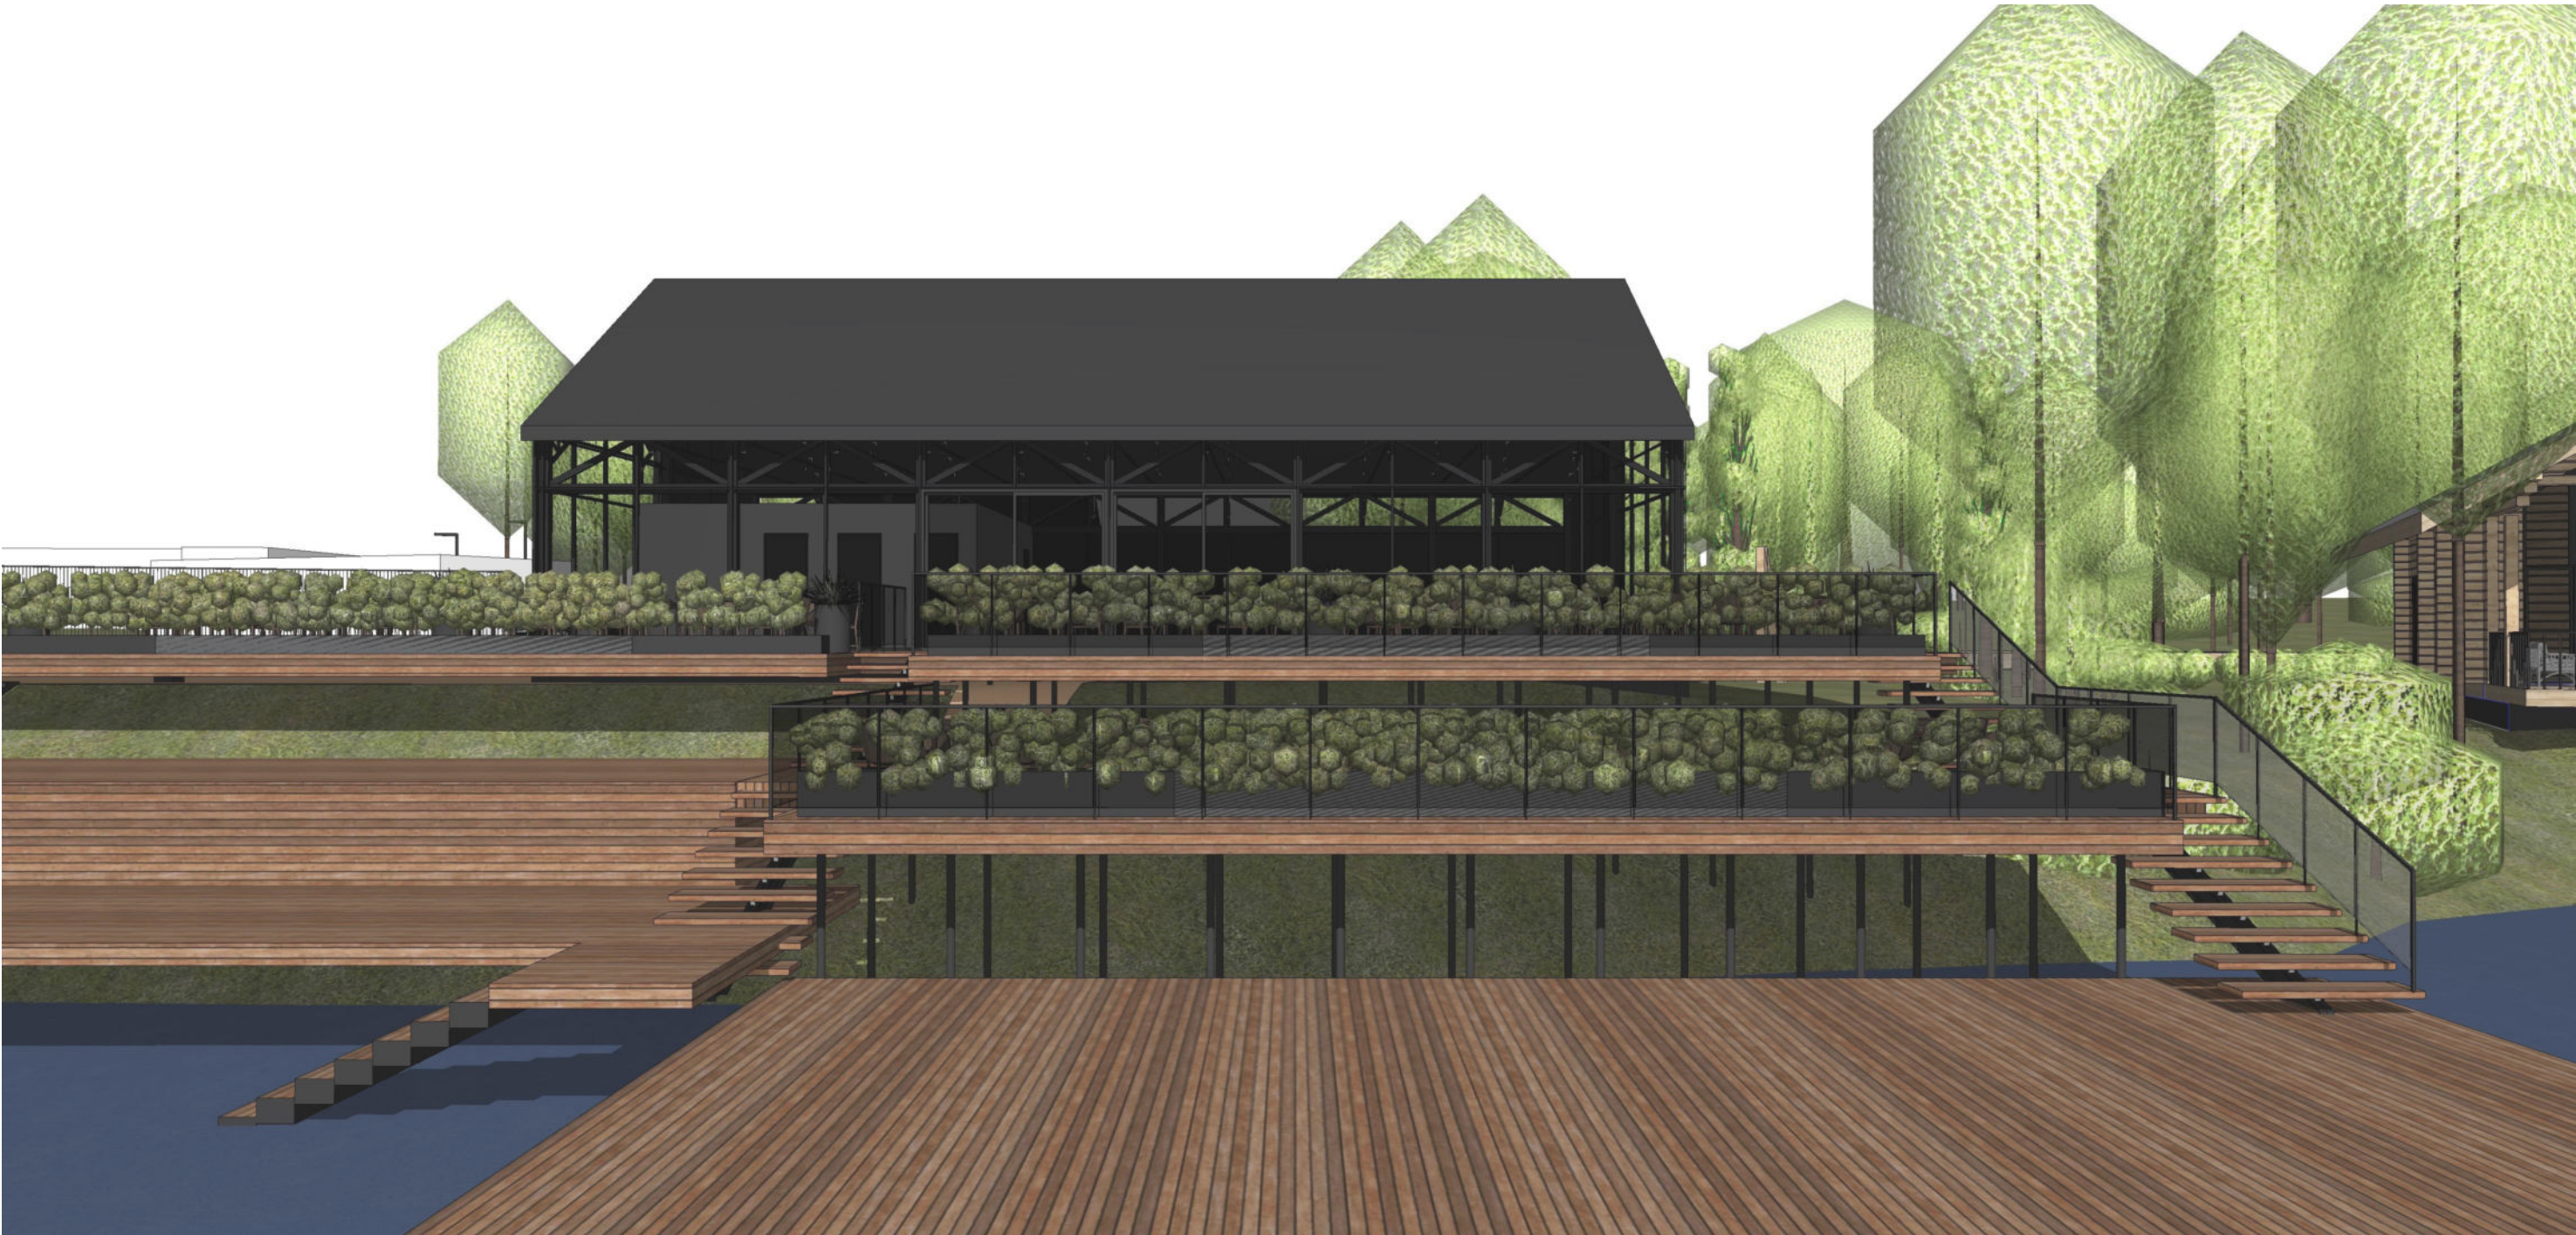


						АР - 1			
						Проект архитектурных решений Экопарка «Красивая поляна» в Демском районе г. Уфа РБ на берегу озера Красивая поляна			
Изм.	Кол.уч.	Лист	№Док.	Подп.	Дата		Стадия	Лист	Листов
Разработал		Закиров			04.2025		АР-1	11	
Проверил		Закиров			04.2025	3D вид ресторана			
Норм. контроль		Закиров			04.2025				

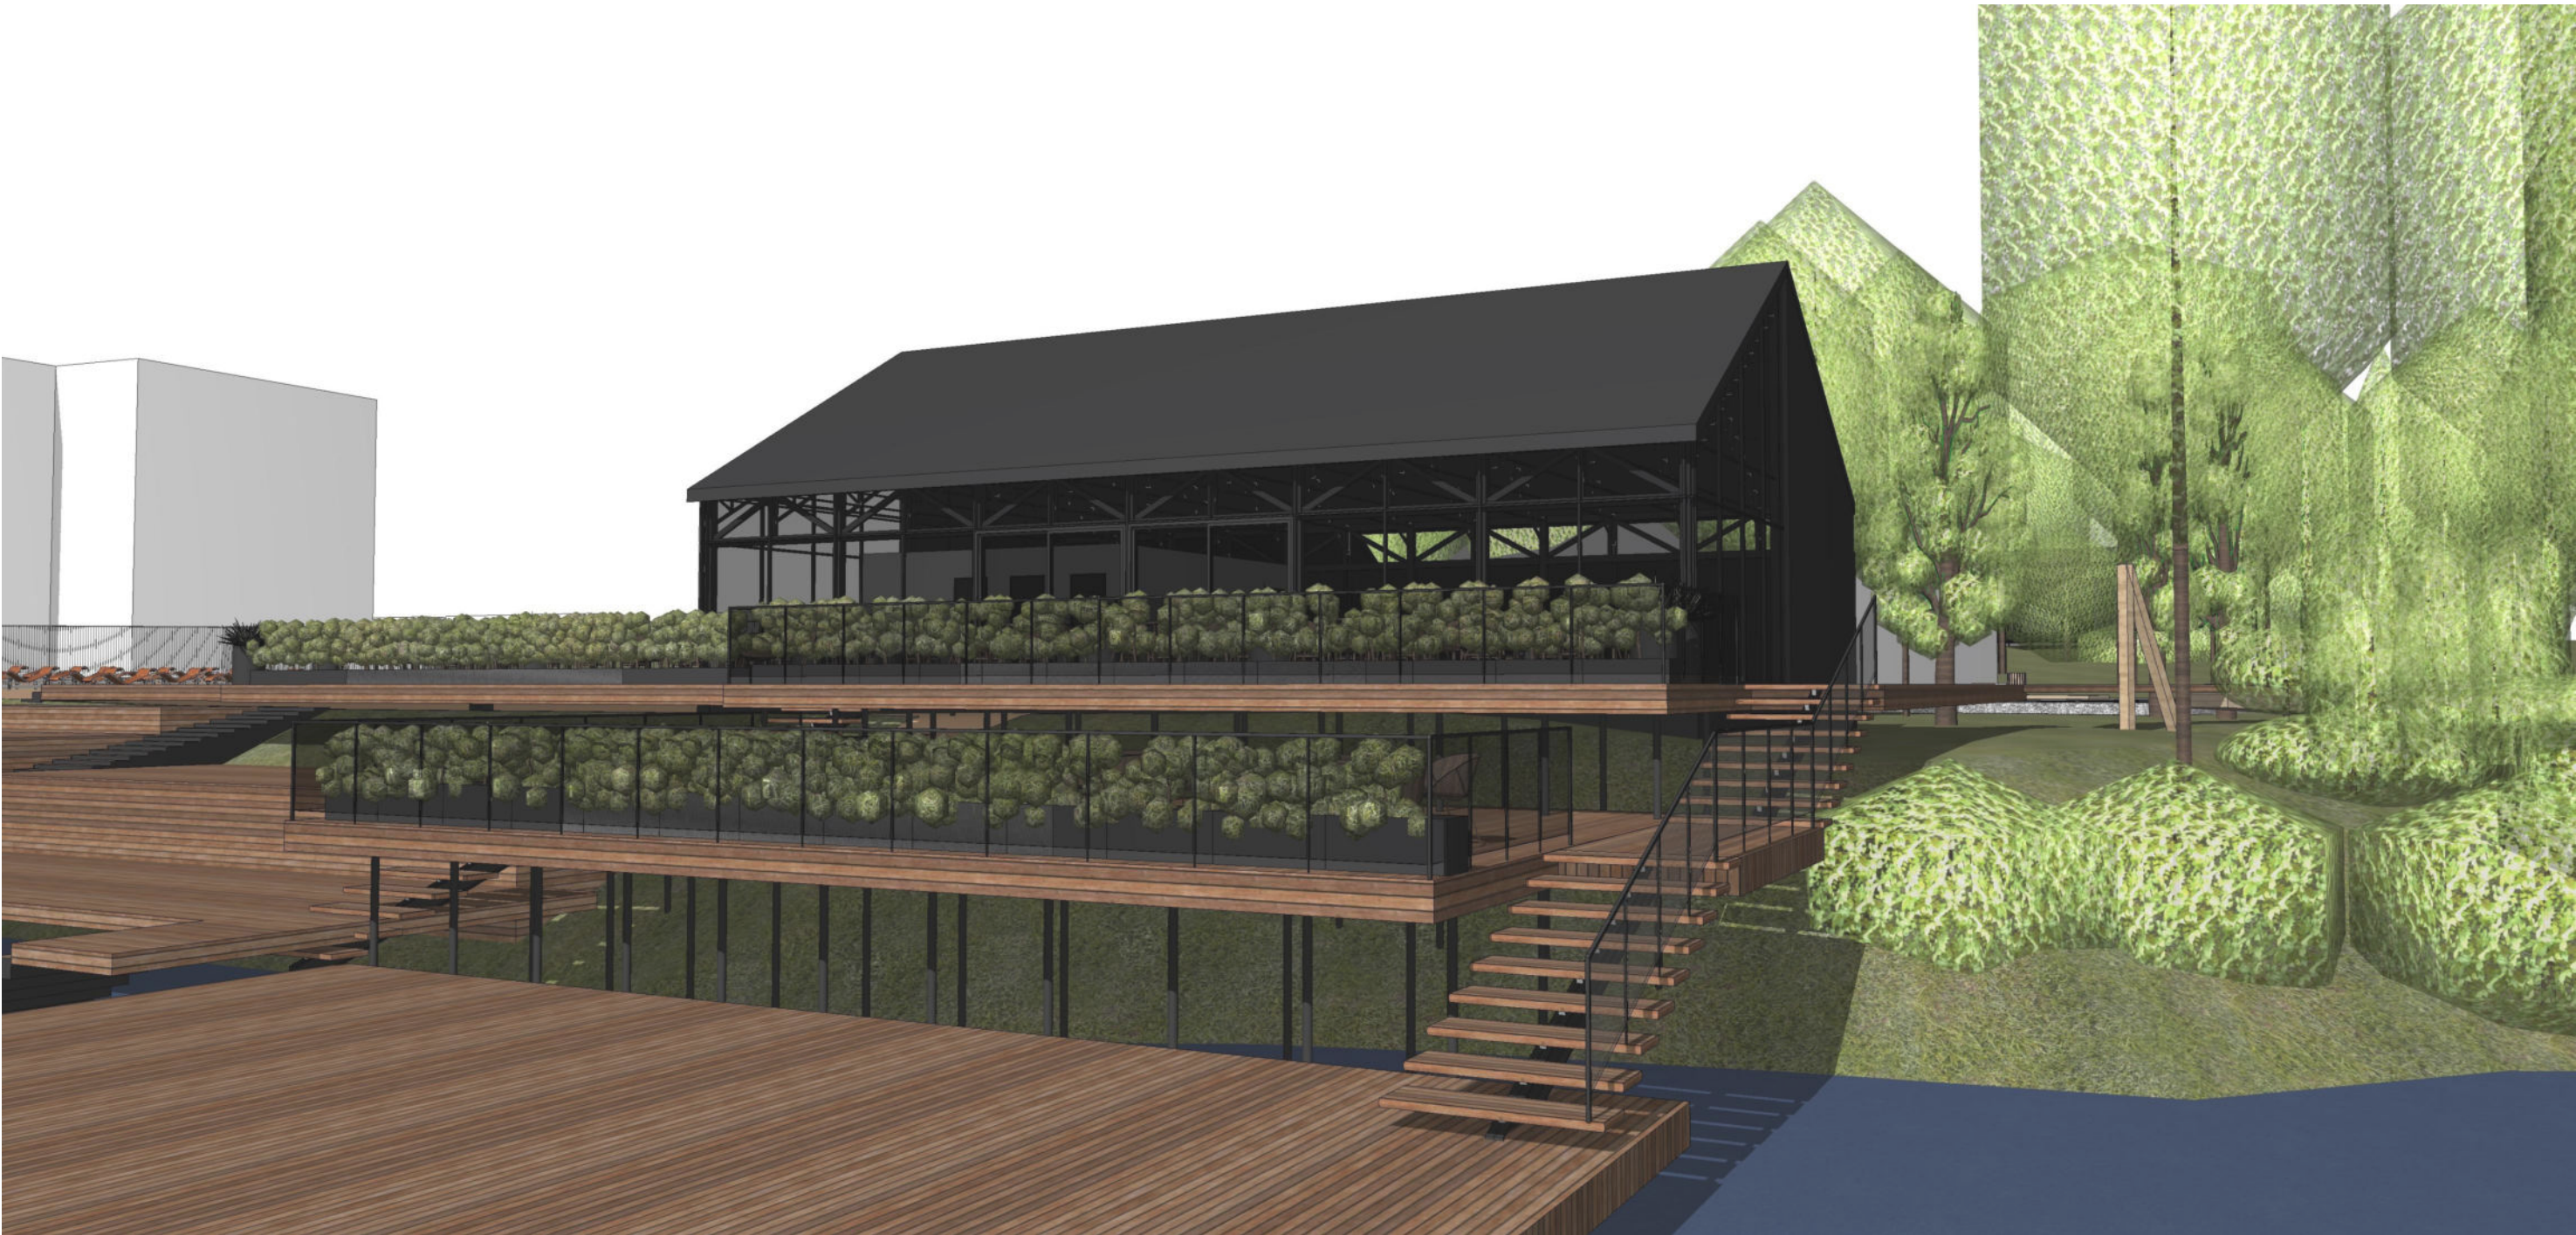


						АР - 1			
						Проект архитектурных решений Экопарка «Красивая поляна» в Демском районе г. Уфа РБ на берегу озера Красивая поляна			
Изм.	Кол.уч.	Лист	№Док.	Подп.	Дата		Стадия	Лист	Листов
Разработал		Закиров			04.2025		АР-1	12	
Проверил		Закиров			04.2025	3D вид ресторана			
Норм. контроль		Закиров			04.2025				

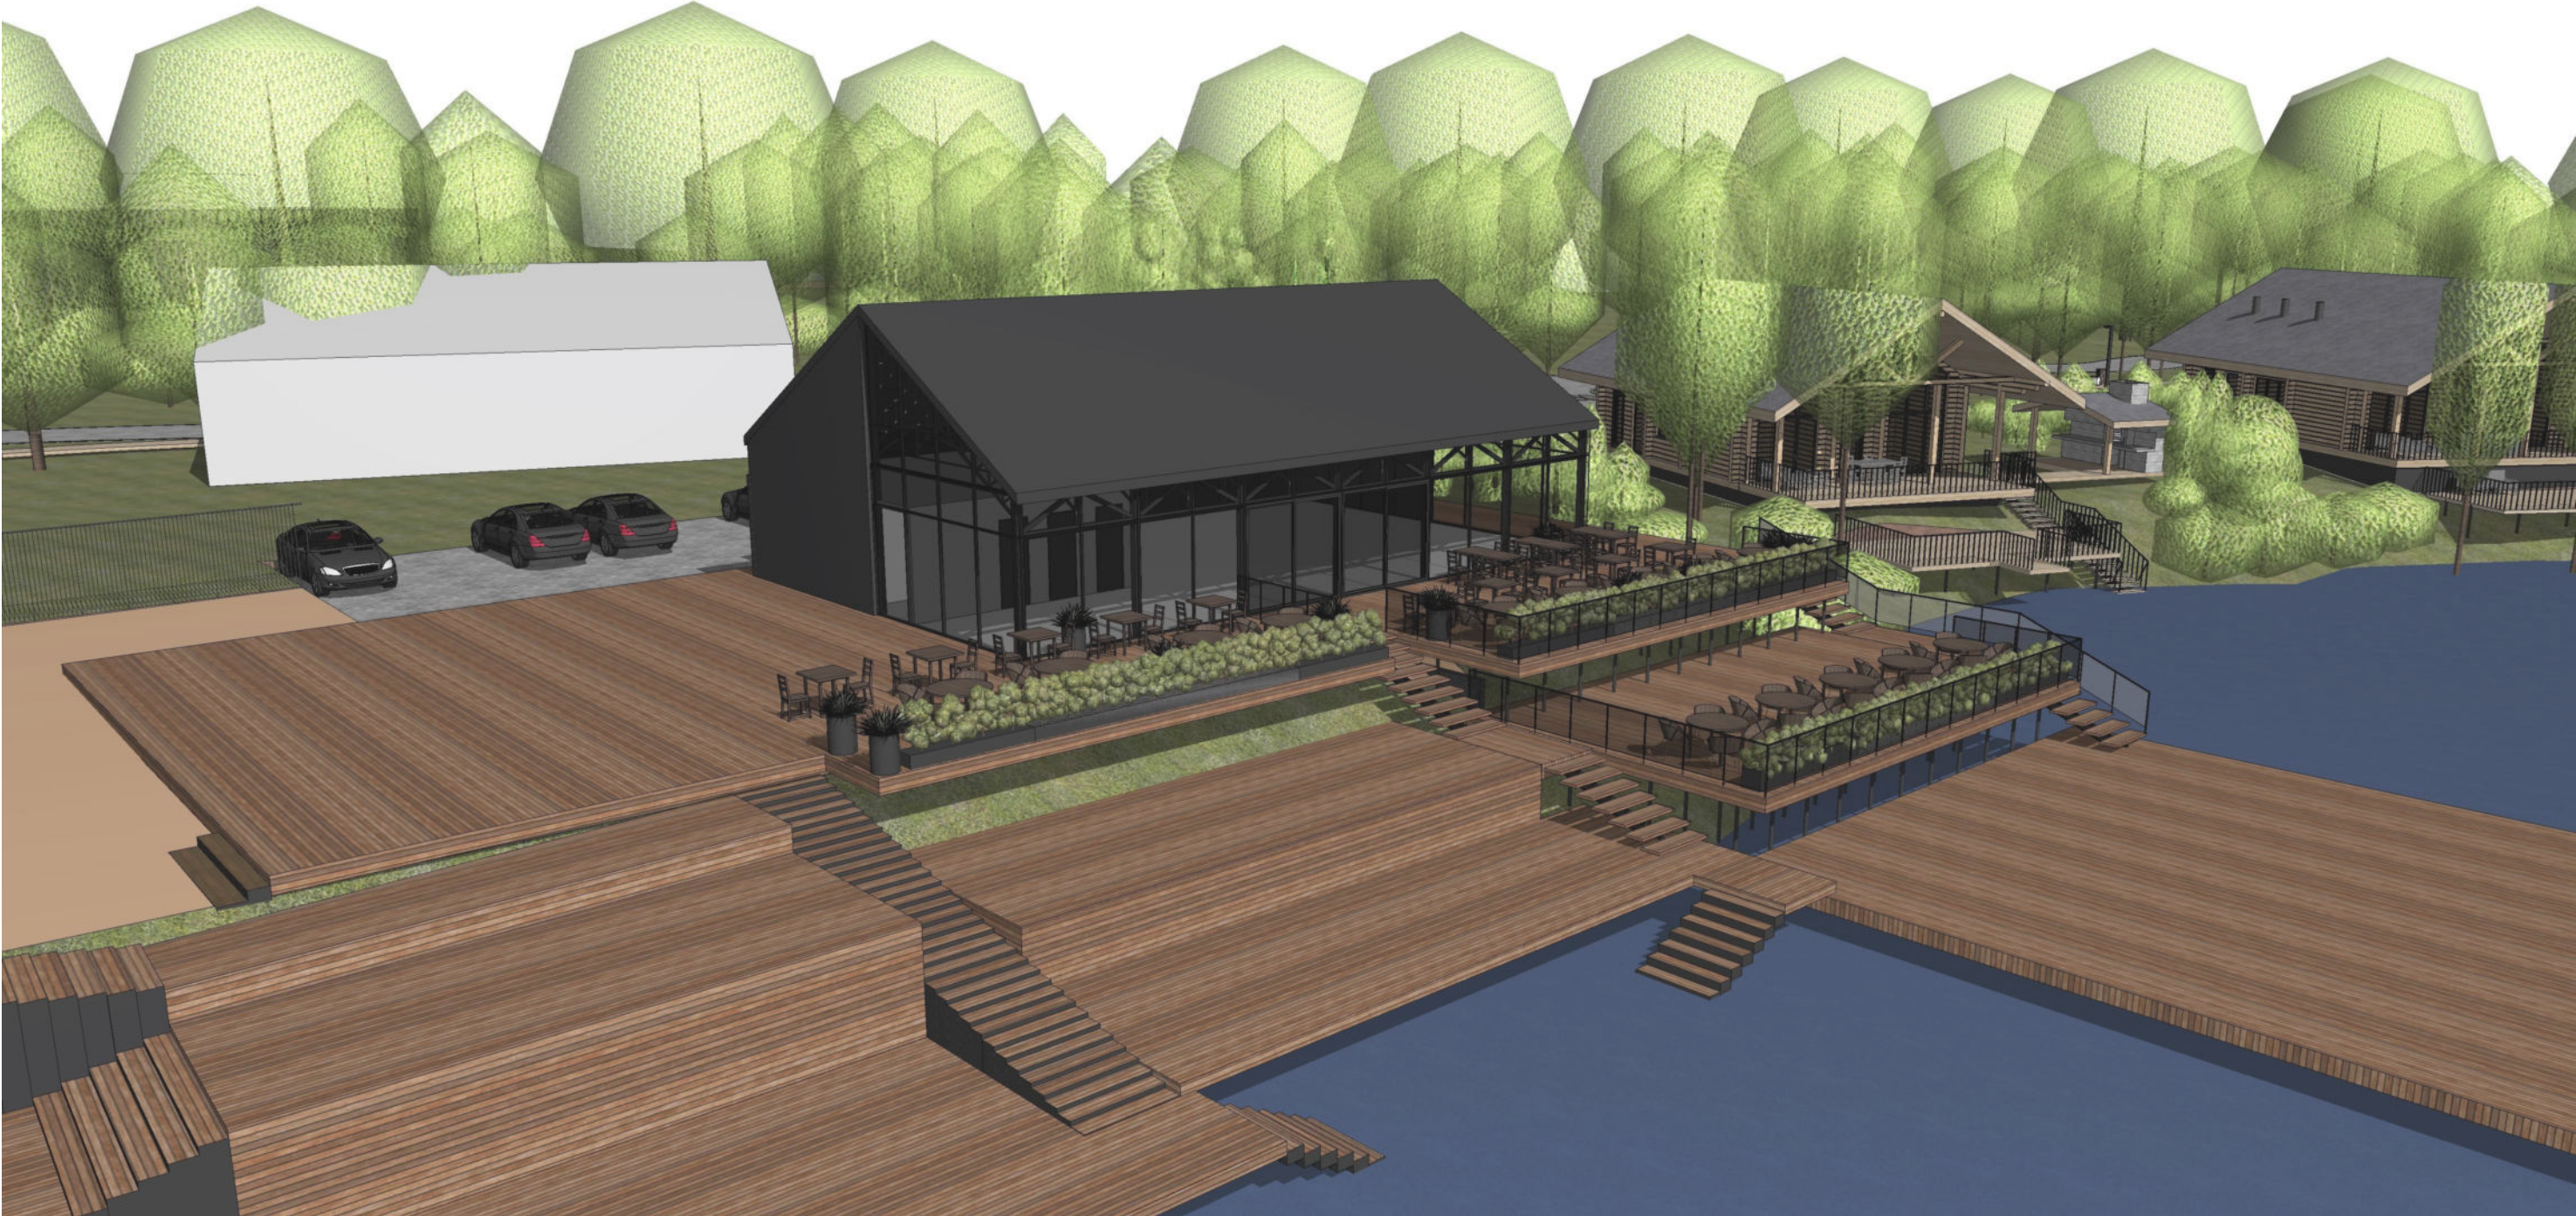

						АР - 1			
						Проект архитектурных решений Экопарка «Красивая поляна» в Демском районе г. Уфа РБ на берегу озера Красивая поляна			
Изм.	Кол.уч.	Лист	№Док.	Подп.	Дата		Стадия	Лист	Листов
Разработал		Закиров			04.2025		АР-1	13	
Проверил		Закиров			04.2025	3D вид ресторана			
Норм. контроль		Закиров			04.2025				

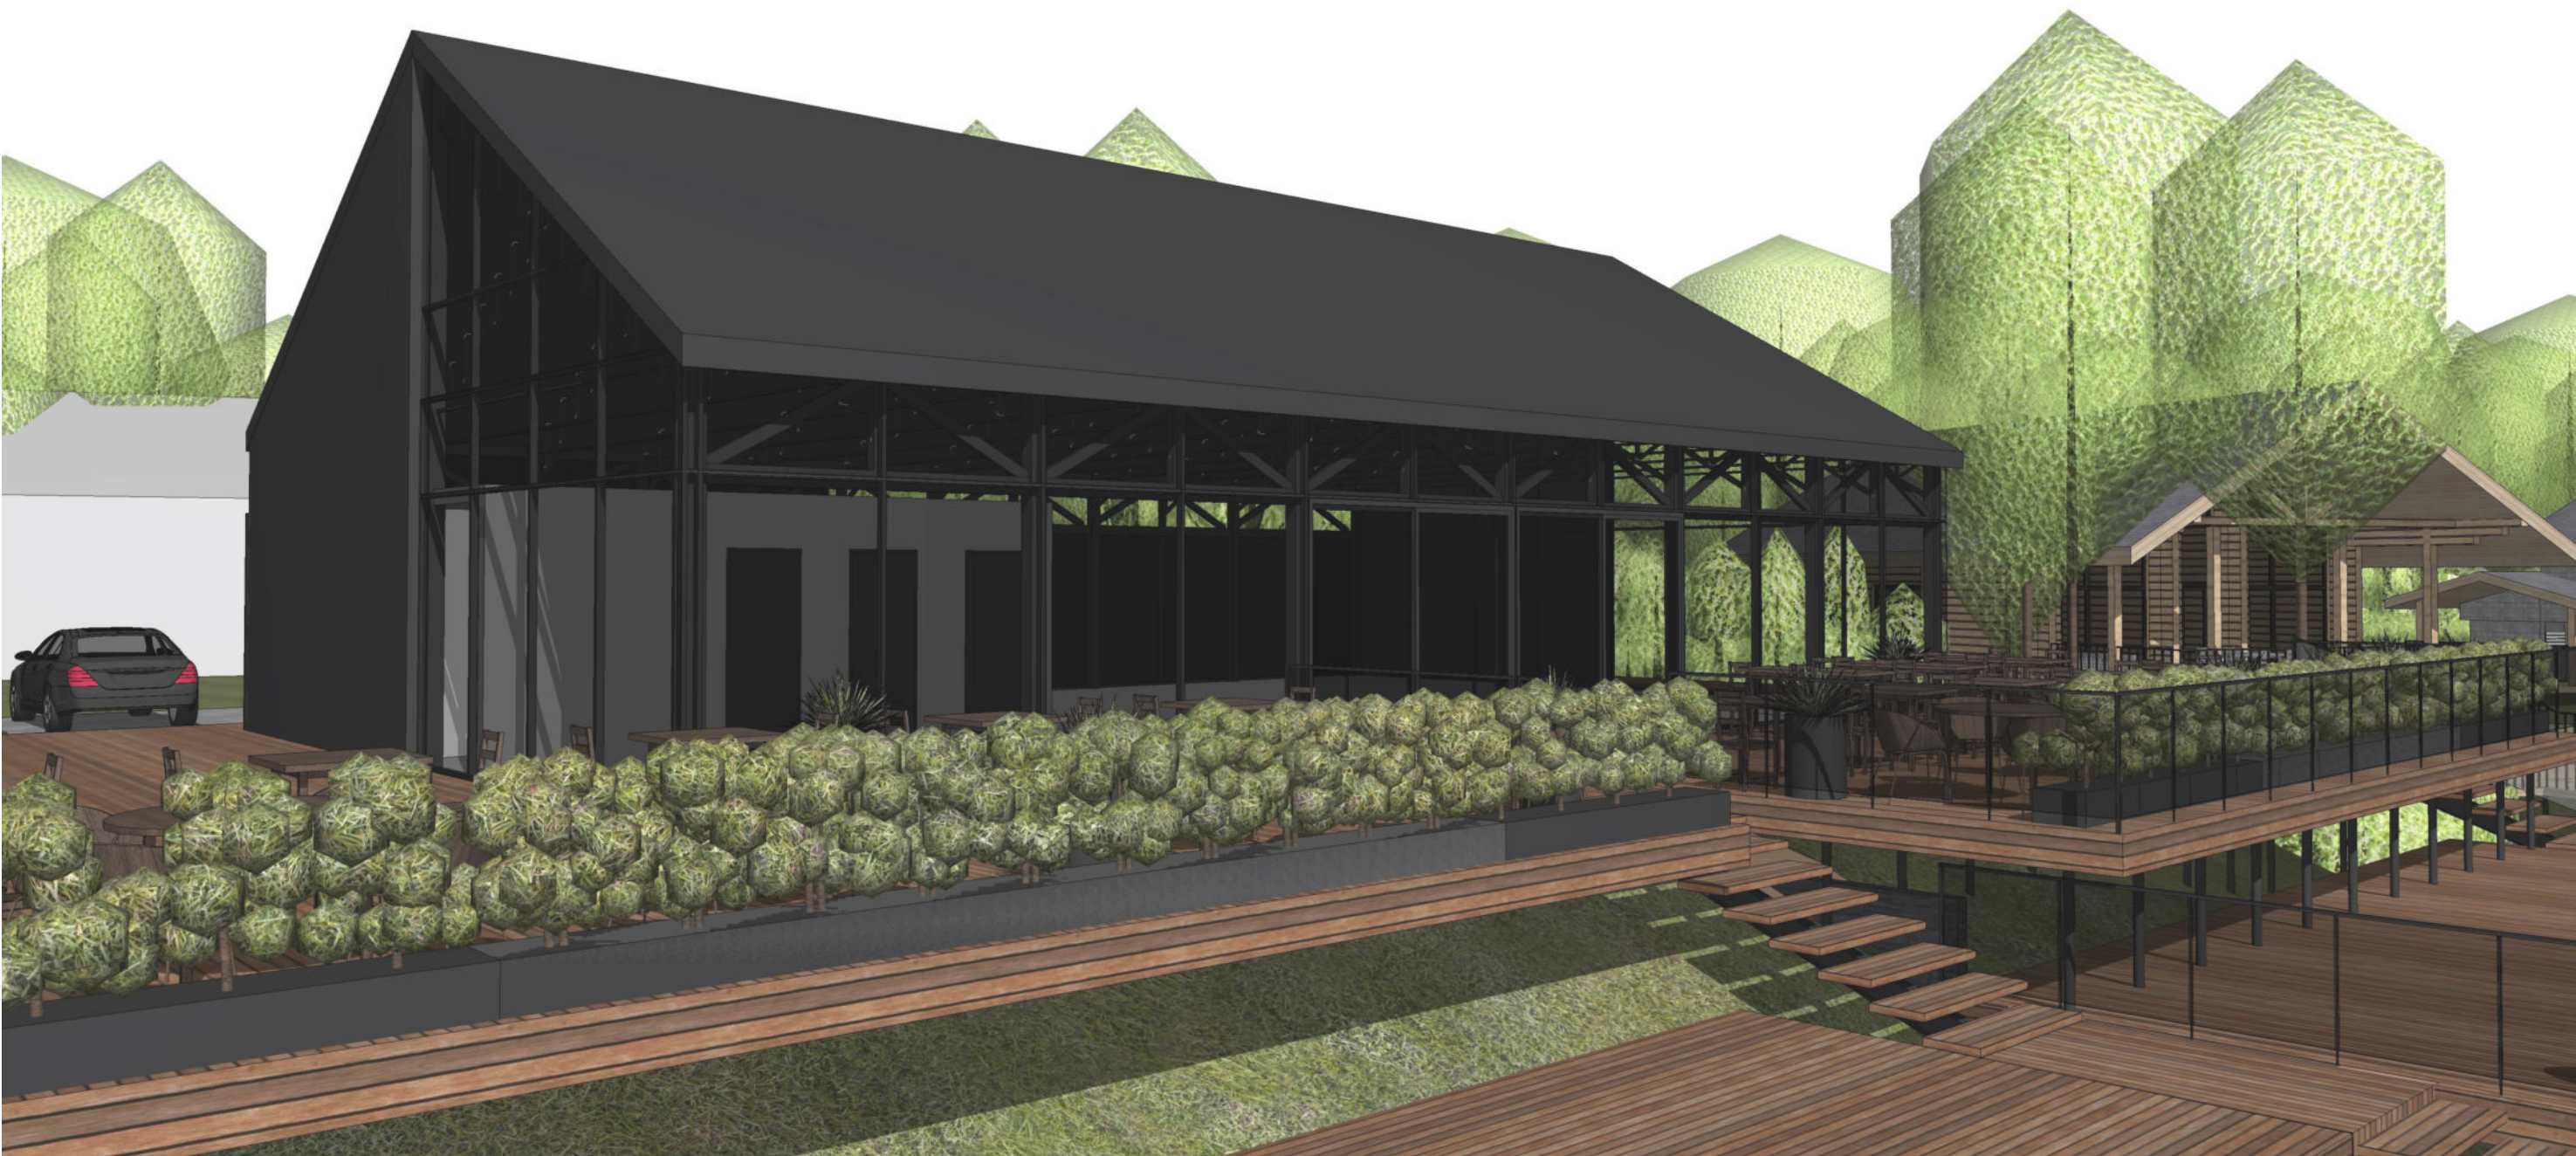

						АР - 1			
						Проект архитектурных решений Экопарка «Красивая поляна» в Демском районе г. Уфа РБ на берегу озера Красивая поляна			
Изм.	Кол.уч.	Лист	№Док.	Подп.	Дата		Стадия	Лист	Листов
Разработал		Закиров			04.2025		АР-1	14	
Проверил		Закиров			04.2025	3D вид ресторана			
Норм. контроль		Закиров			04.2025				

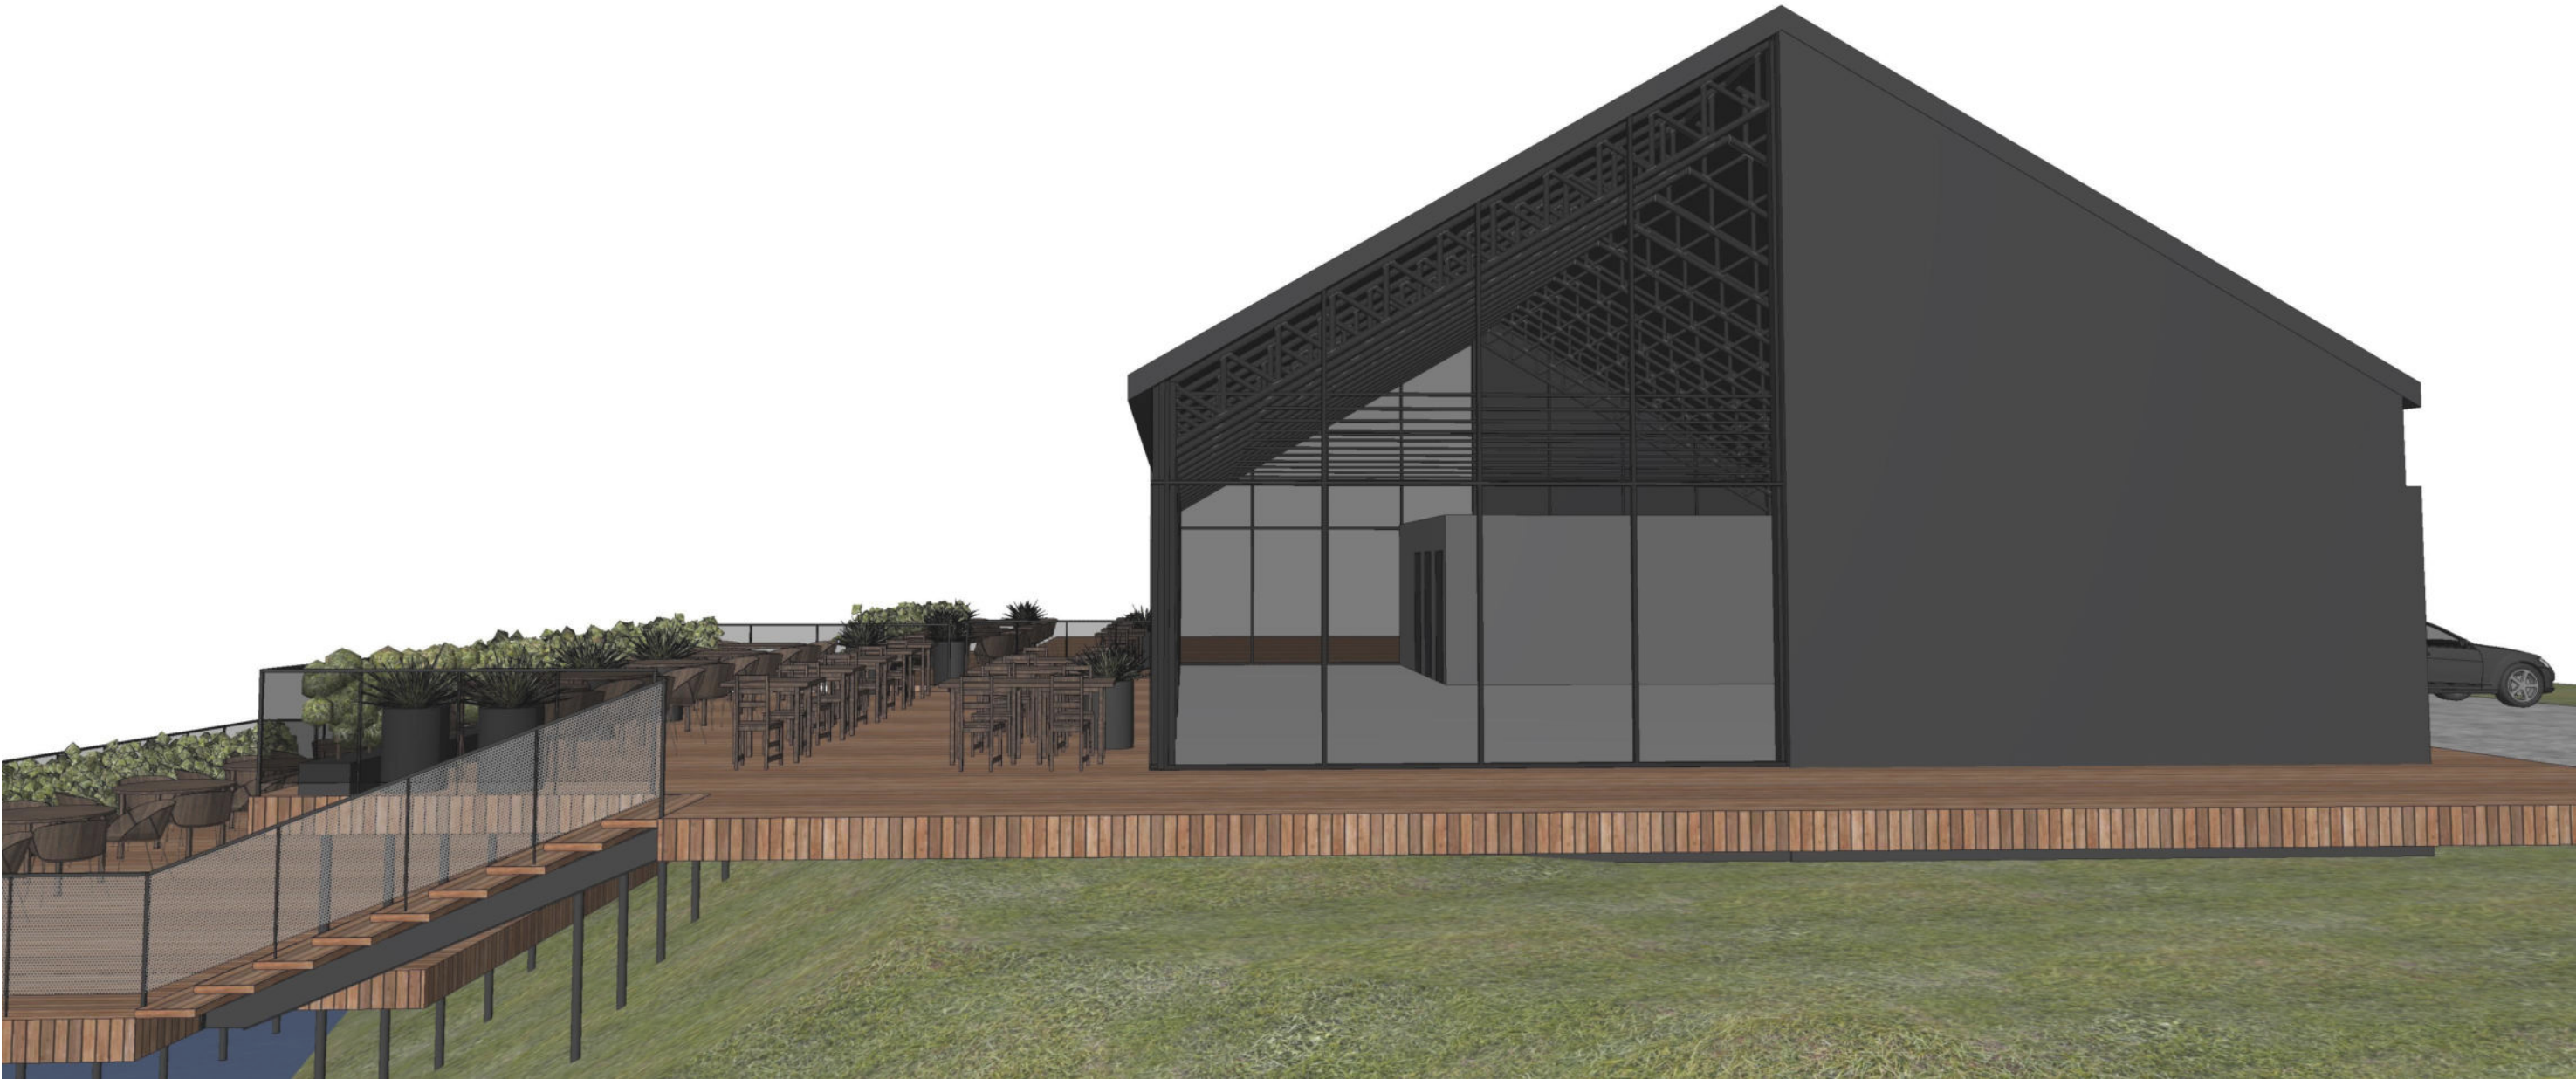


						АР - 1			
						Проект архитектурных решений Экопарка «Красивая поляна» в Демском районе г. Уфа РБ на берегу озера Красивая поляна			
Изм.	Кол.уч.	Лист	№Док.	Подп.	Дата		Стадия	Лист	Листов
Разработал		Закиров			04.2025		АР-1	15	
Проверил		Закиров			04.2025	3D вид ресторана			
Норм. контроль		Закиров			04.2025				




						АР - 1			
						Проект архитектурных решений Экопарка «Красивая поляна» в Демском районе г. Уфа РБ на берегу озера Красивая поляна			
Изм.	Кол.уч.	Лист	№Док.	Подп.	Дата		Стадия	Лист	Листов
Разработал		Закиров			04.2025		АР-1	16	
Проверил		Закиров			04.2025	3D вид ресторана			
Норм. контроль		Закиров			04.2025				



						АР - 1			
						Проект архитектурных решений Экопарк «Красивая поляна» в Демском районе г. Уфа РБ на берегу озера Красивая поляна			
Изм.	Кол.уч.	Лист	№Док.	Подп.	Дата		Стадия	Лист	Листов
Разработал		Закиров			04.2025		АР-1	17	
Проверил		Закиров			04.2025	3D вид ресторана			
Норм. контроль		Закиров			04.2025				

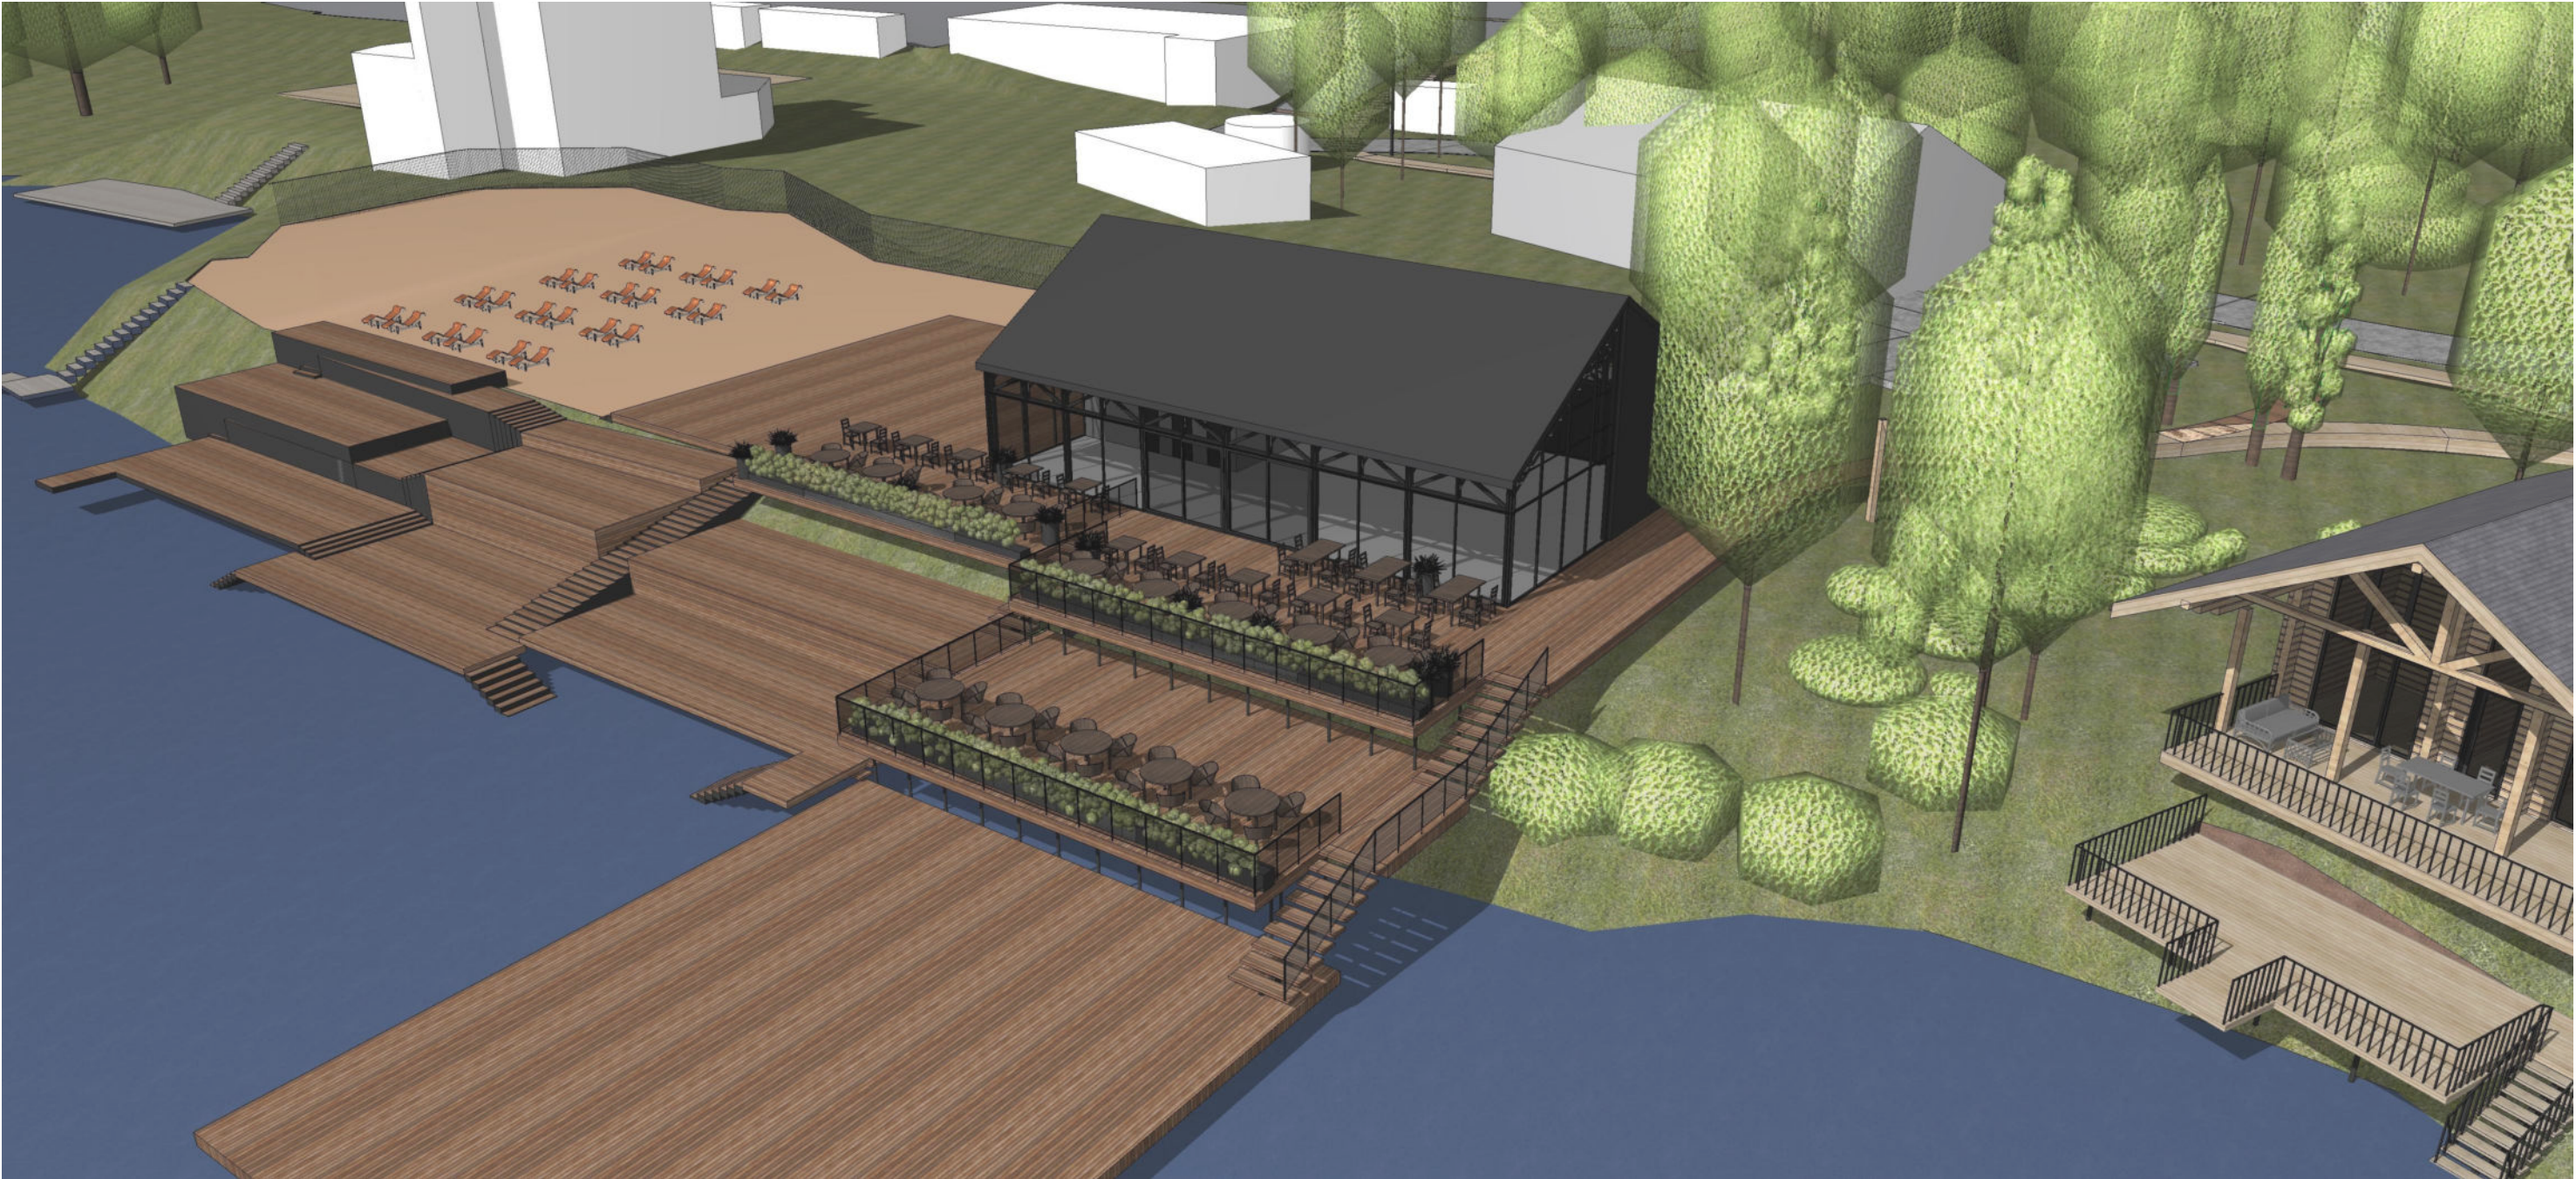


						АР - 1			
						Проект архитектурных решений Экопарка «Красивая поляна» в Демском районе г. Уфа РБ на берегу озера Красивая поляна			
Изм.	Кол.уч.	Лист	№Док.	Подп.	Дата		Стадия	Лист	Листов
Разработал		Закиров			04.2025		АР-1	18	
Проверил		Закиров			04.2025	3D вид ресторана			
Норм. контроль		Закиров			04.2025				

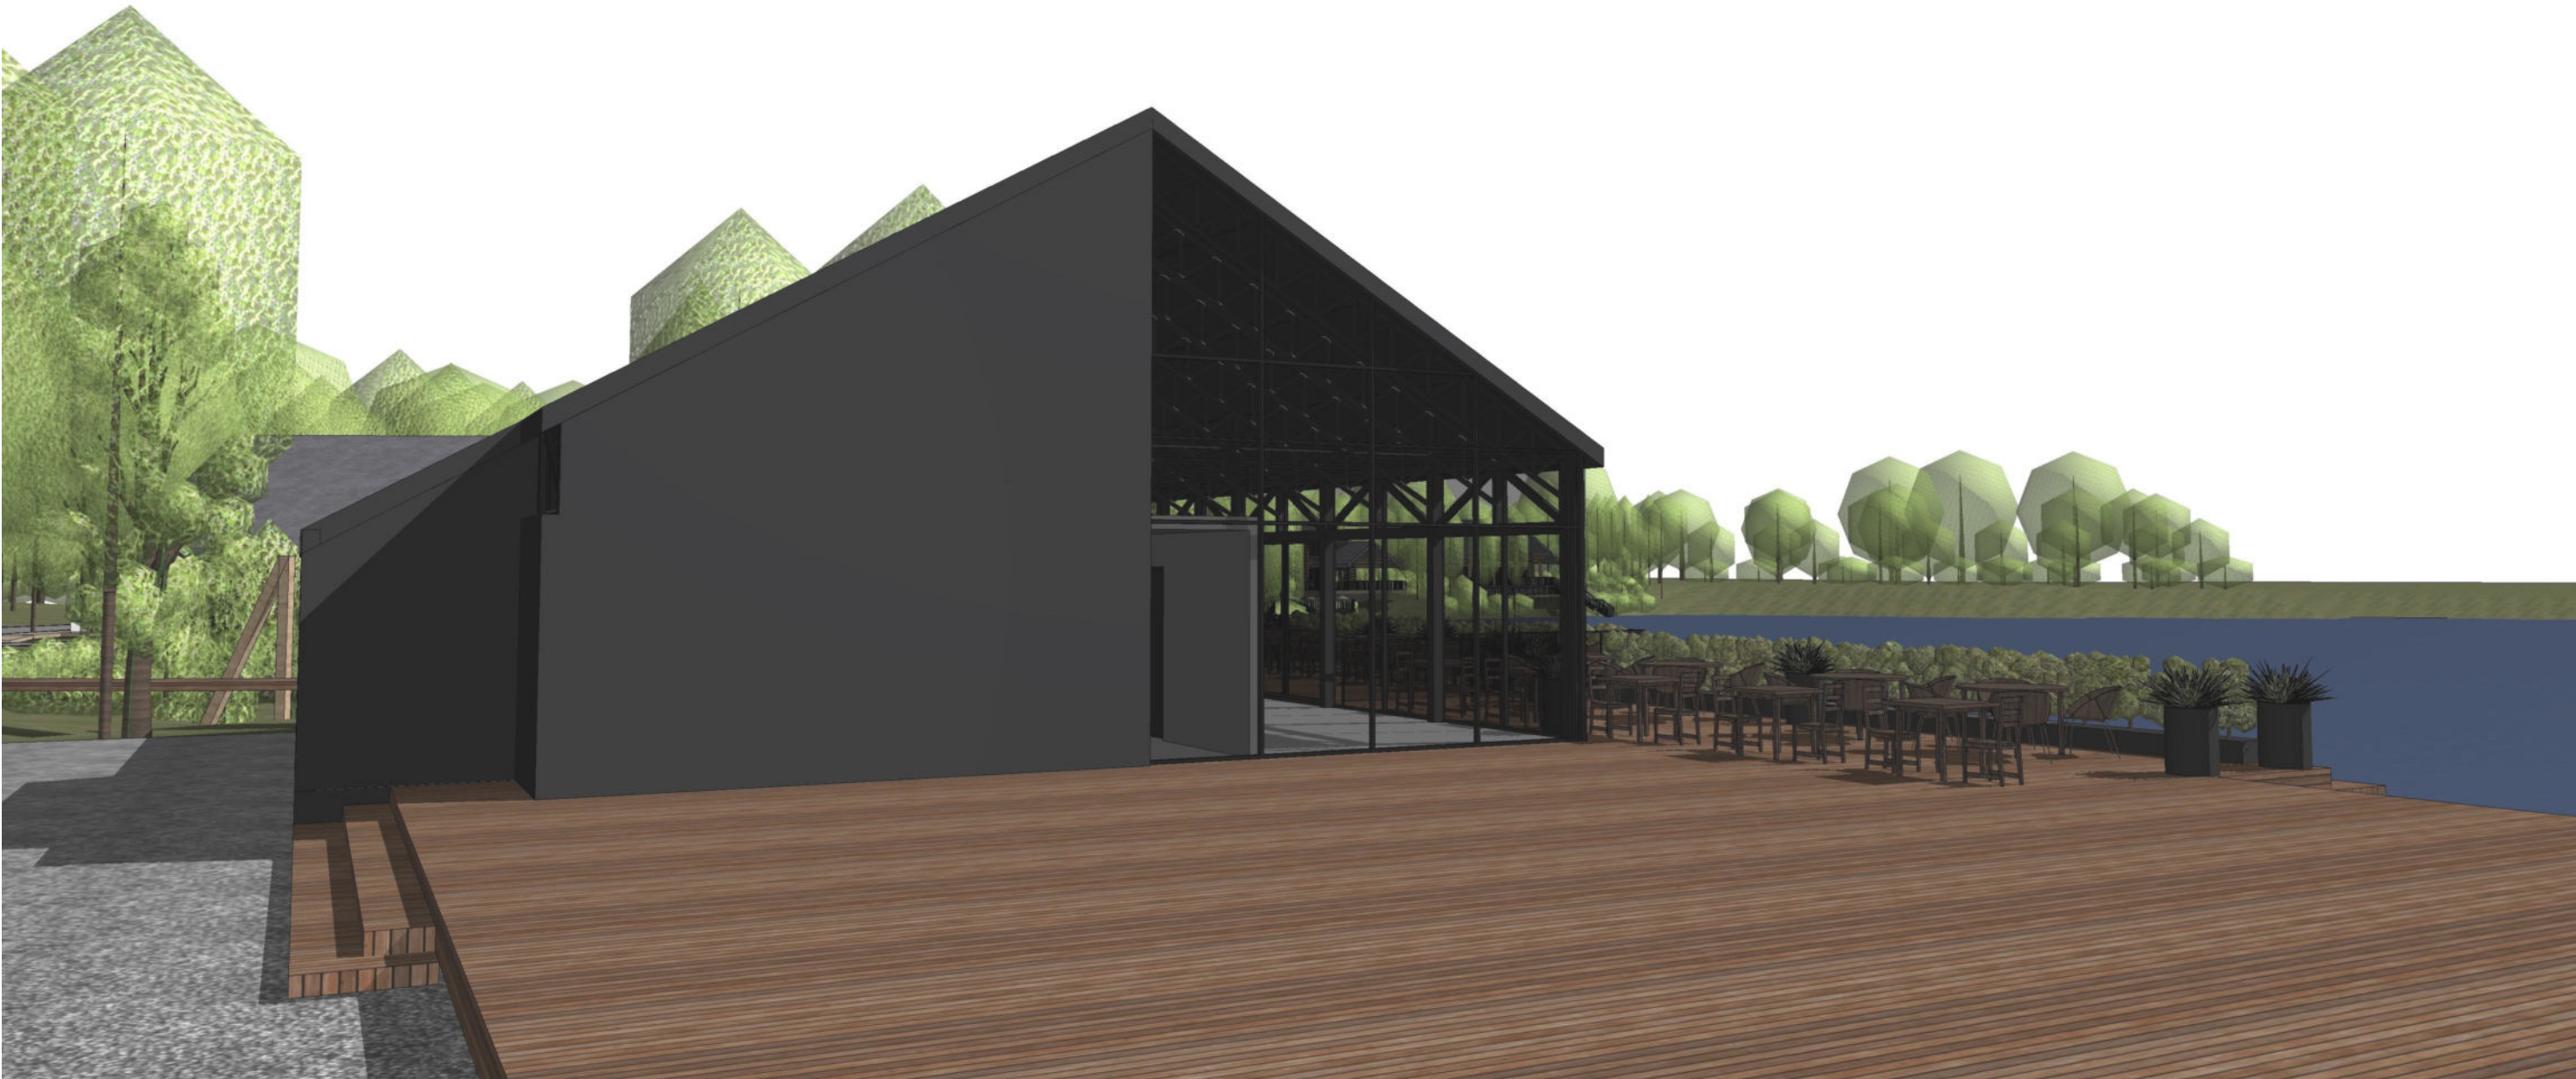


						АР - 1			
						Проект архитектурных решений Экопарк «Красивая поляна» в Демском районе г. Уфа РБ на берегу озера Красивая поляна			
Изм.	Кол.уч.	Лист	№Док.	Подп.	Дата		Стадия	Лист	Листов
Разработал		Закиров			04.2025		АР-1	19	
Проверил		Закиров			04.2025	3D вид ресторана			
Норм. контроль		Закиров			04.2025				

План МС

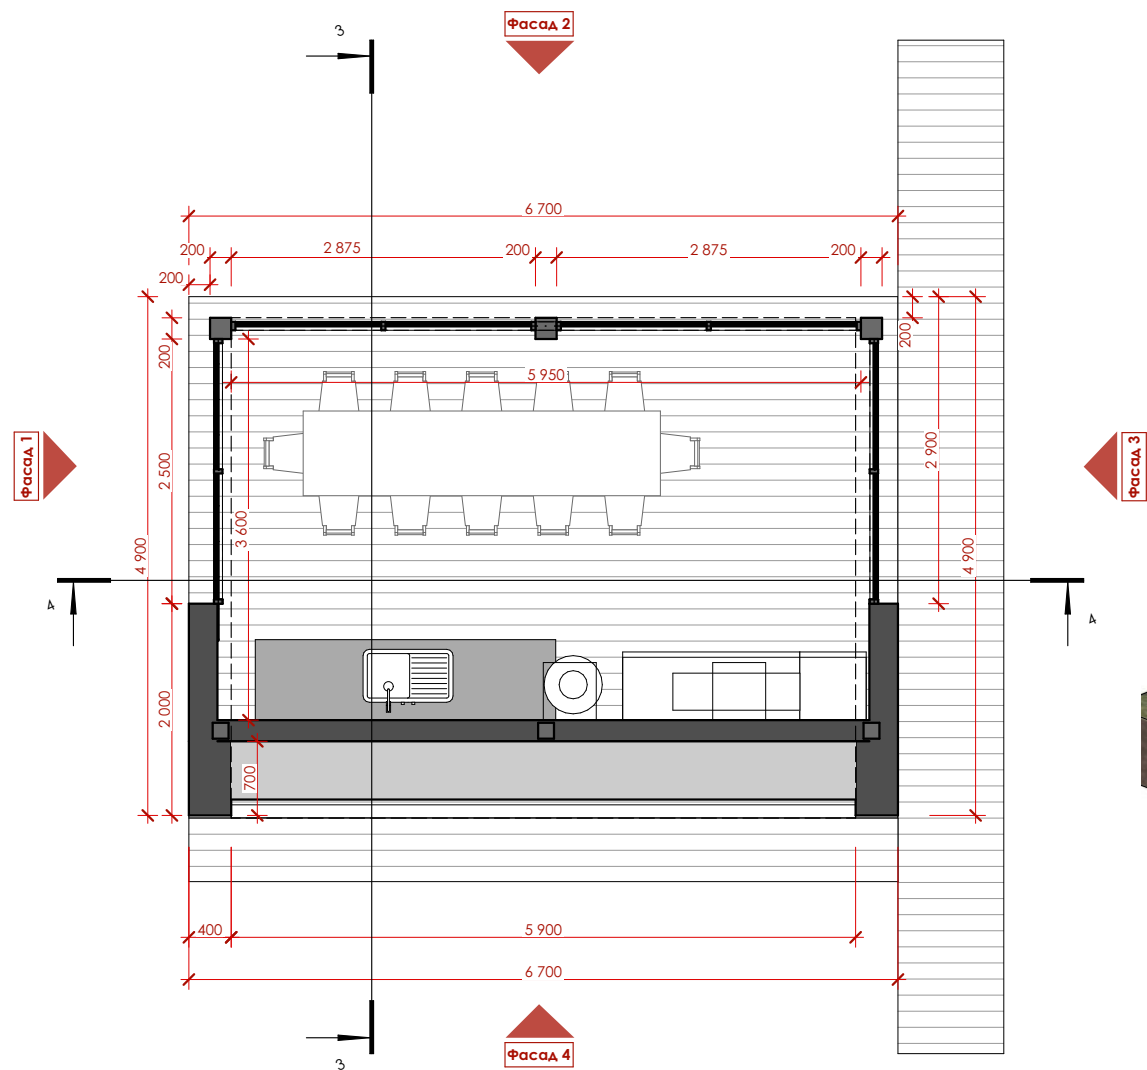


Аксонометрия мангальной зоны

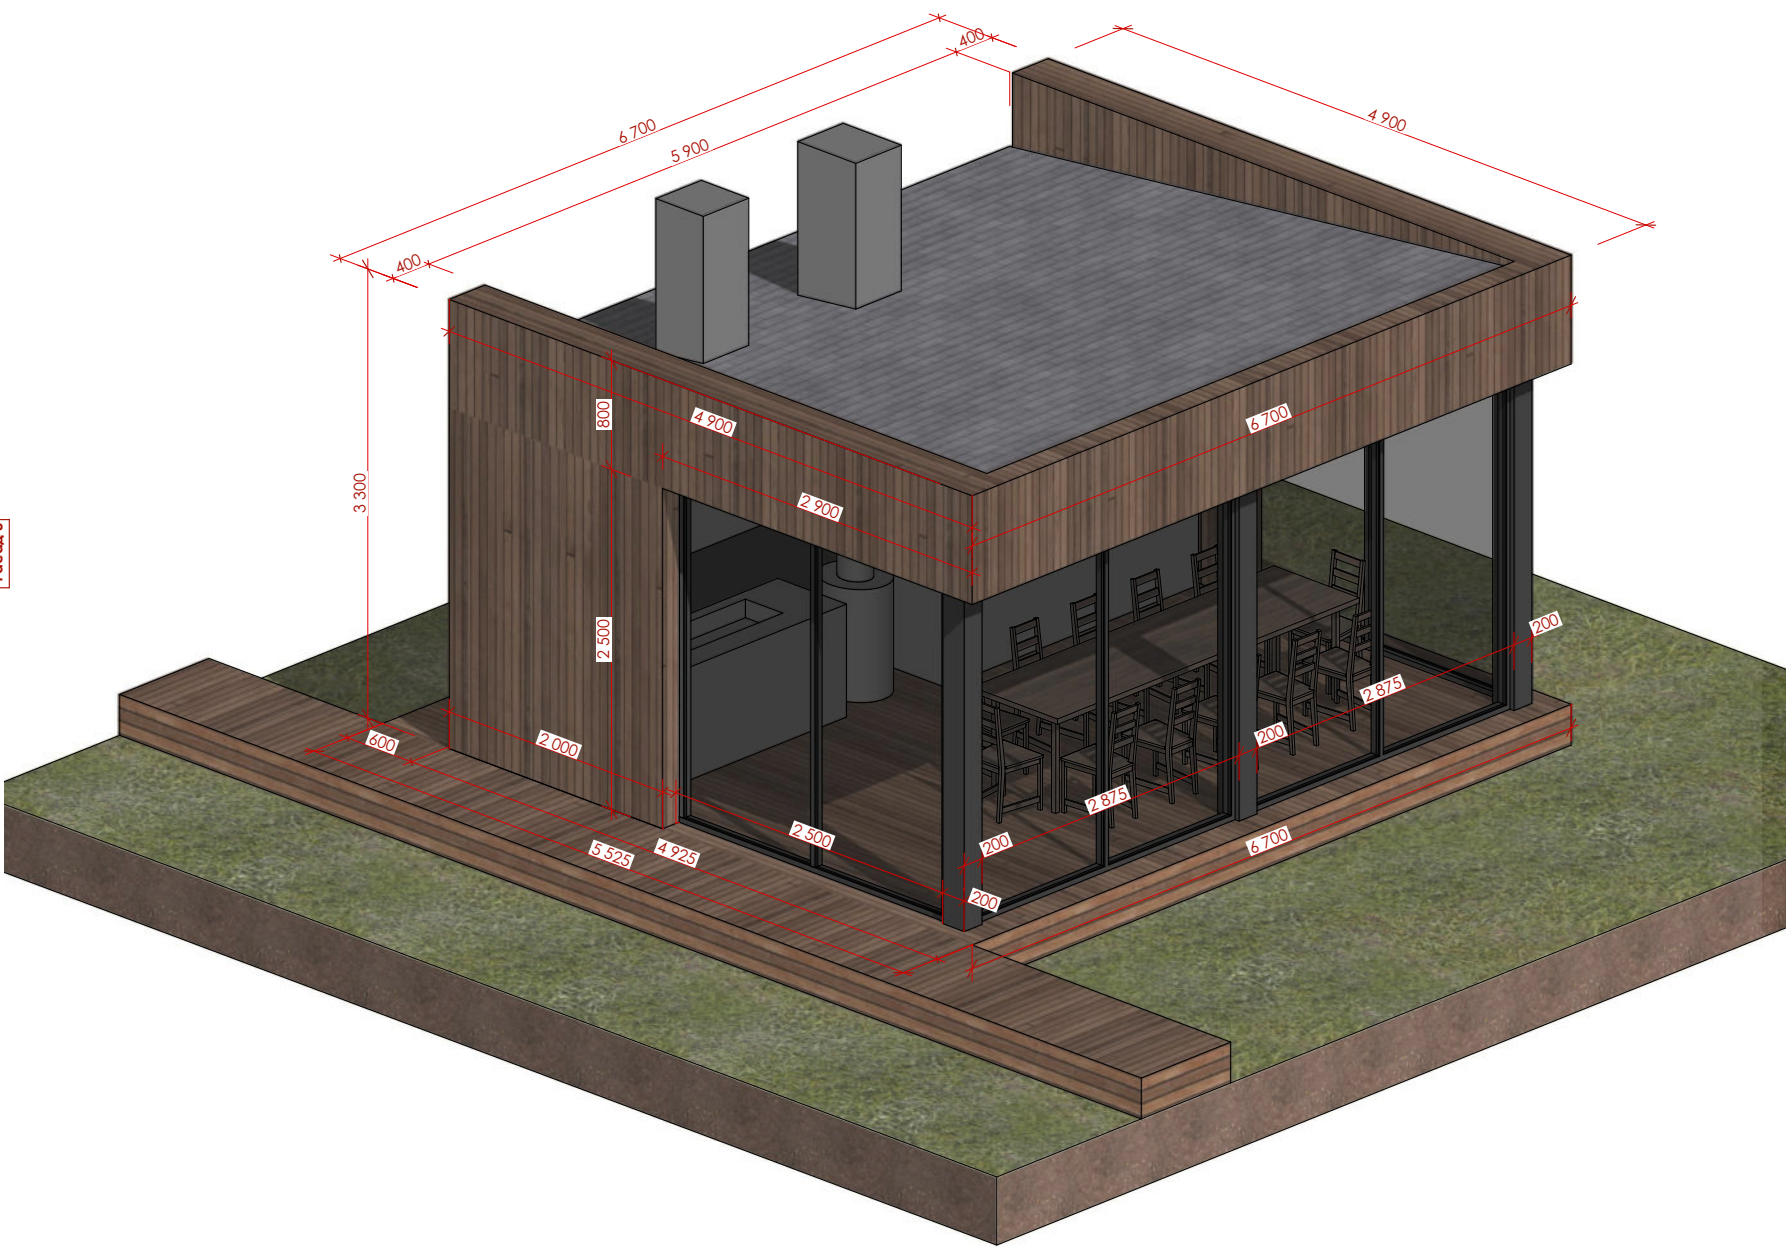


- Примечания:
1. За 0.000 принять уровень пола беседки.
 2. Конструктивные узлы, толщины утеплителя, размеры конструкций определить со специалистами.
 3. Количество и расположение вентиляционных каналов/дымохода определить со специалистами.
 4. Вент. каналы/дымоход выполнить герметично и вывести на необходимую высоту предварительно проконсультировавшись со специалистами.
 5. Конструктивные узлы, толщины утеплителя, размеры конструкций определить со специалистами.
 6. Для строительства террасы вокруг рекомендуется использовать металлические сваи в качестве основы конструкции.
 7. Рамы окон выполнить в цвете RAL 7024/7022, перед заказом снять замеры, согласовать с авторами проекта.
 8. Данные чертежи не носят технический характер и не являются строительными.


						АР - 1			
						Проект архитектурных решений Экопарка «Красивая поляна» в Демском районе г. Уфа РБ на берегу озера Красивая поляна			
Изм.	Кол.уч.	Лист	№Док.	Подп.	Дата	Разработал	Стадия	Лист	Листов
					04.2025		АР-1	20	
Проверил		Закиров			04.2025	План беседки с мангалом			
Норм. контроль		Закиров			04.2025				

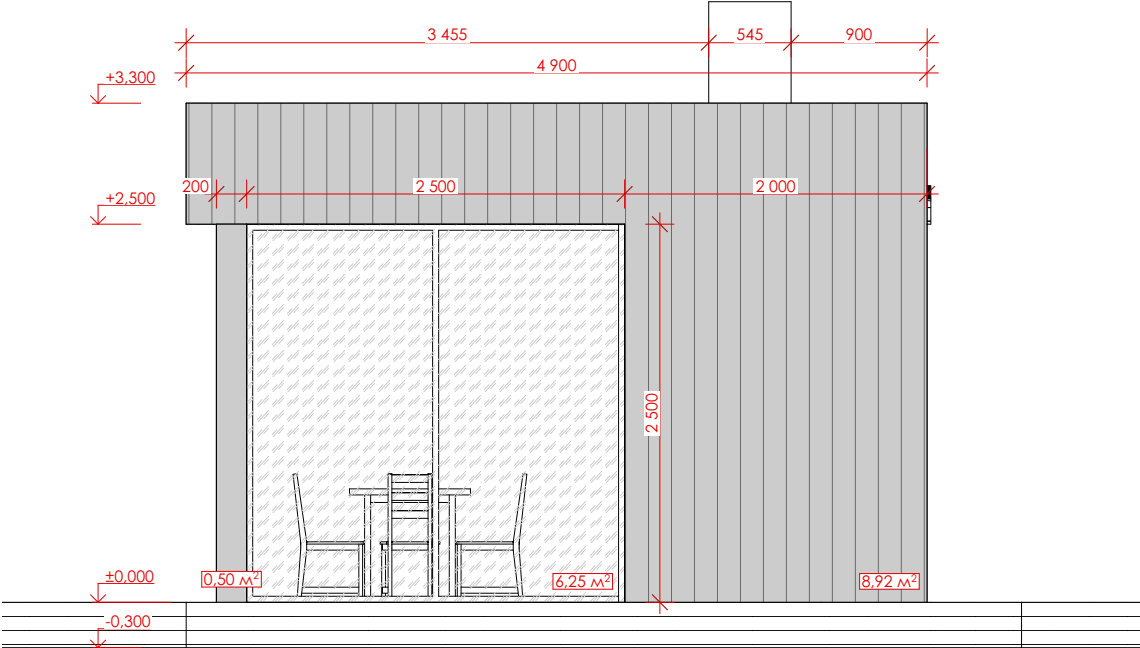


Фасад 1

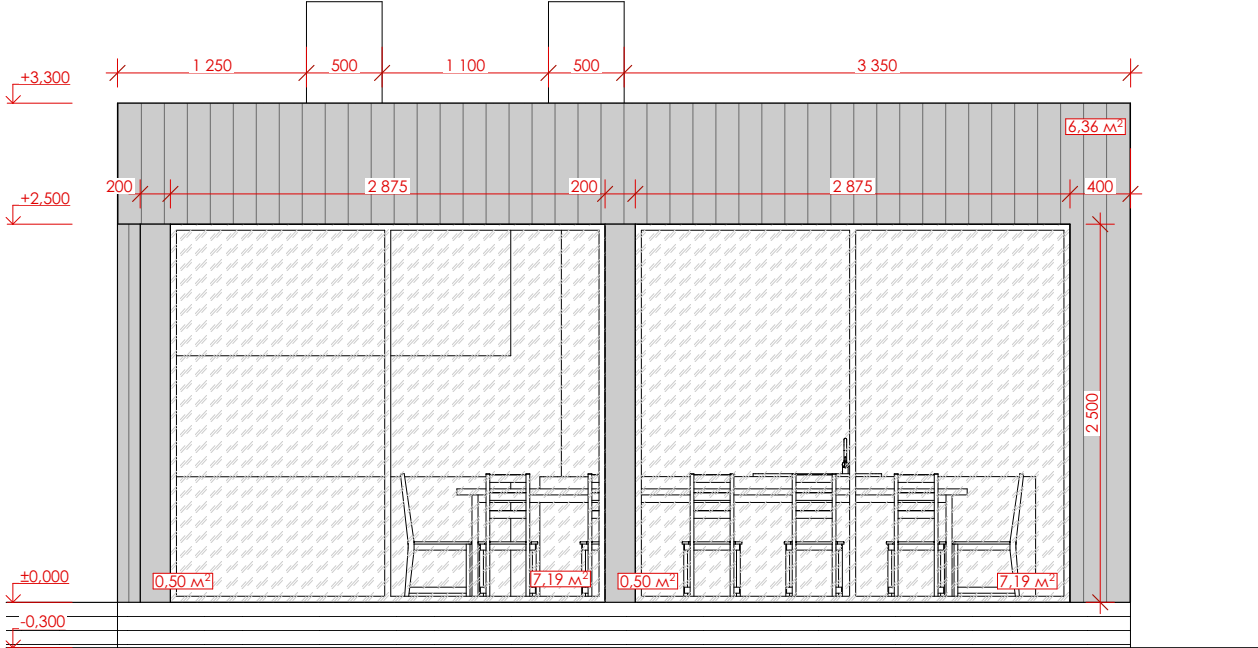

Фасад 2

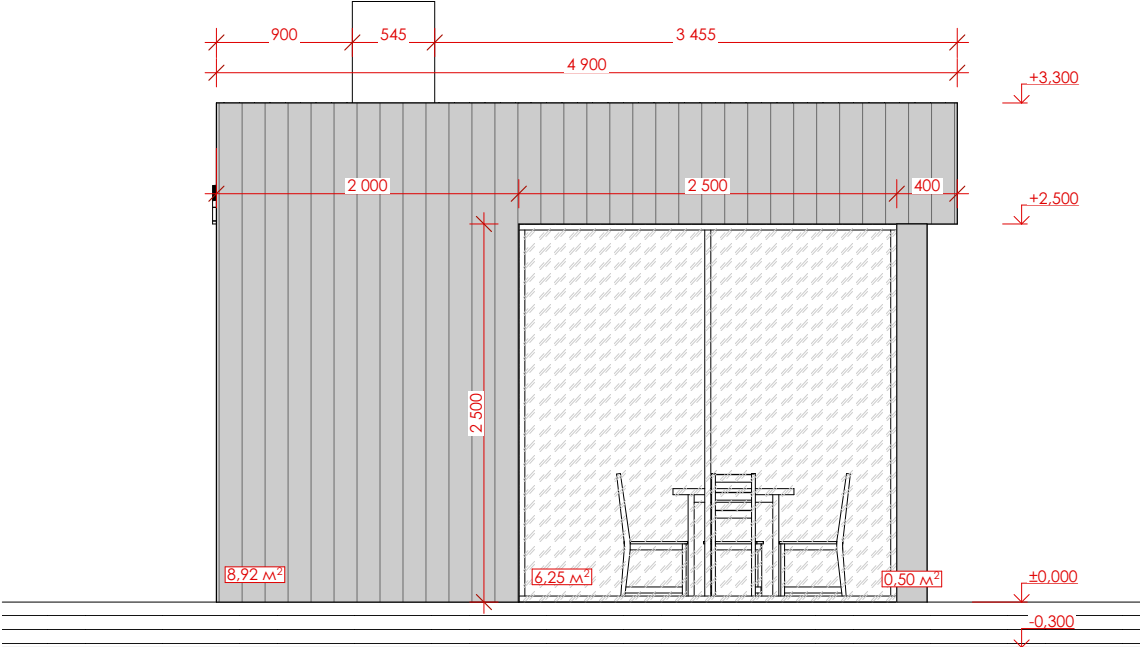


Фасад 3

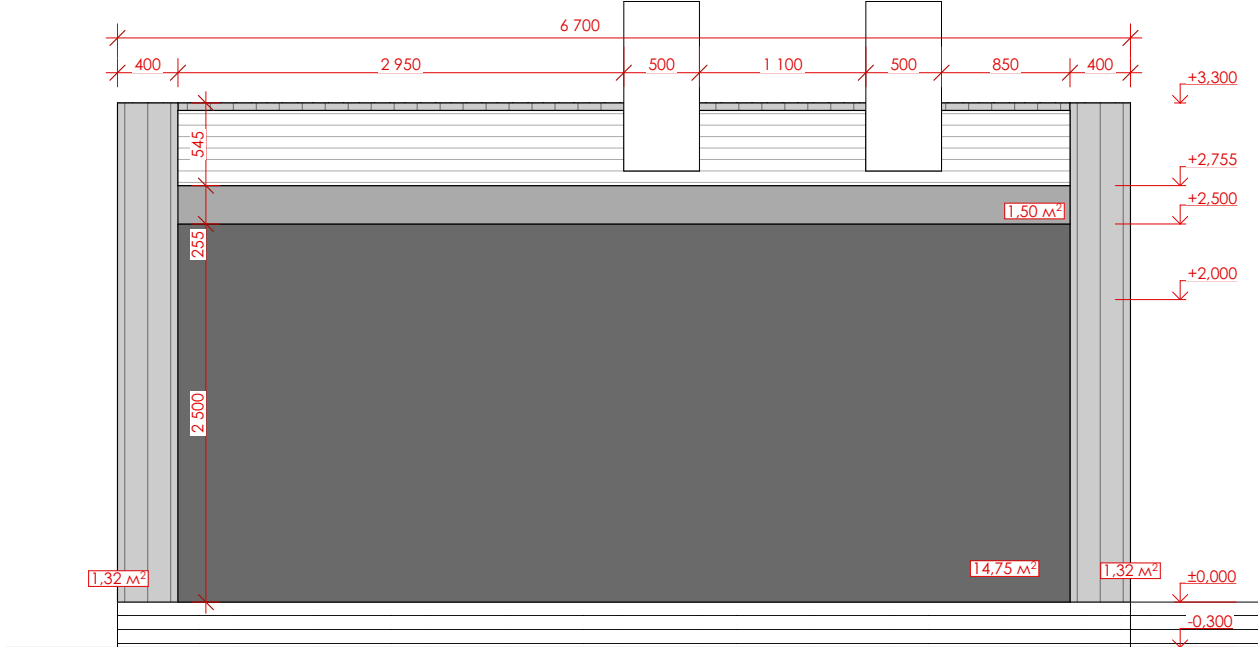


Фасад 4

Примечания:
1. За 0.000 принять уровень пола беседки.
2. Конструктивные узлы, толщины утеплителя, размеры конструкций определить со специалистами.
3. Количество и расположение вентиляционных каналов/дымохода определить со специалистами.
4. Вент. каналы/дымоход выполнить герметично и вывести на необходимую высоту предварительно проконсультировавшись со специалистами.
5. Конструктивные узлы, толщины утеплителя, размеры конструкций определить со специалистами.
6. Для строительства террасы вокруг рекомендуется использовать металлические сваи в качестве основы конструкции.
7. Рамы окон выполнить в цвете RAL 7024/7022, перед заказом снять замеры, согласовать с авторами проекта.
8. Данные чертежи не носят технический характер и не являются строительными.

						АР - 1			
						Проект архитектурных решений Экопарка «Красивая поляна» в Демском районе г. Уфа РБ на берегу озера Красивая поляна			
Изм.	Кол.уч.	Лист	№Док.	Подп.	Дата		Стадия	Лист	Листов
Разработал	Закиров				04.2025		АР-1	21	
Проверил	Закиров				04.2025	Фасады беседки			
Норм. контроль	Закиров				04.2025				

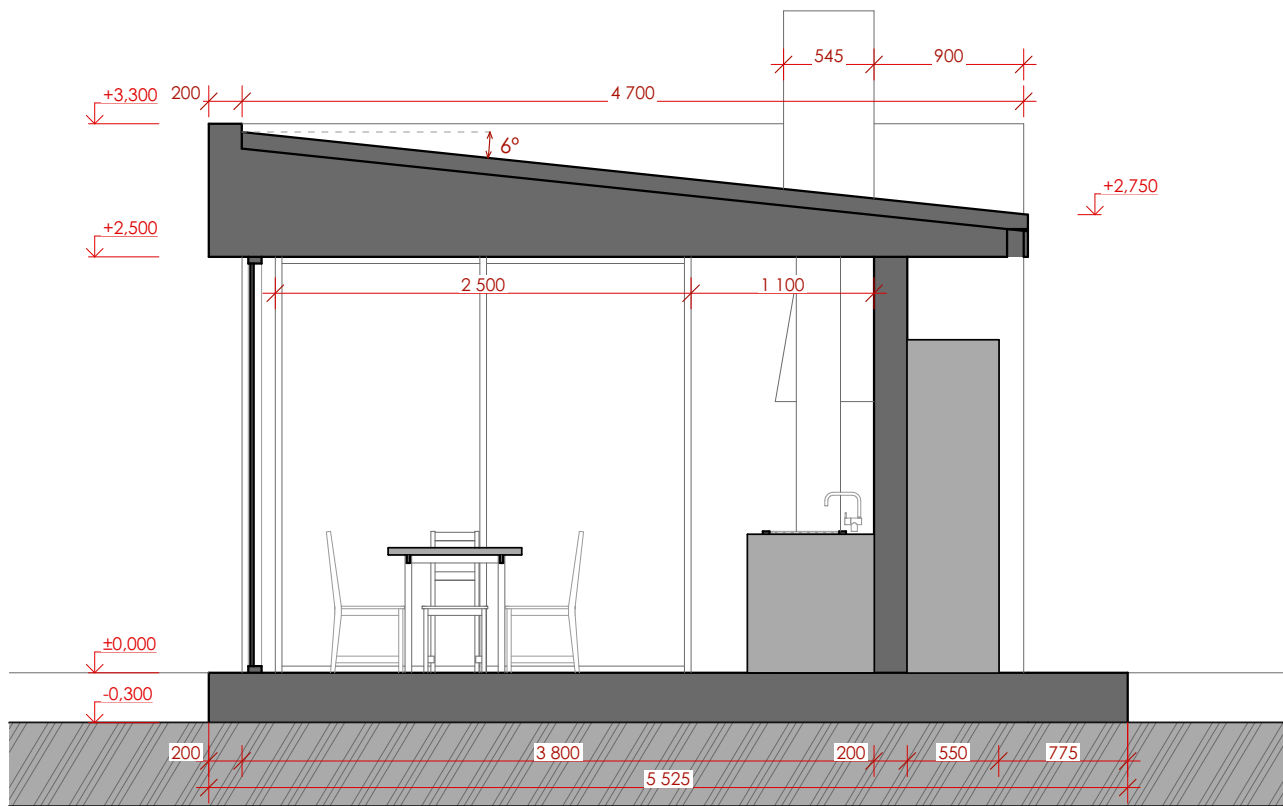


Разрез 3-3

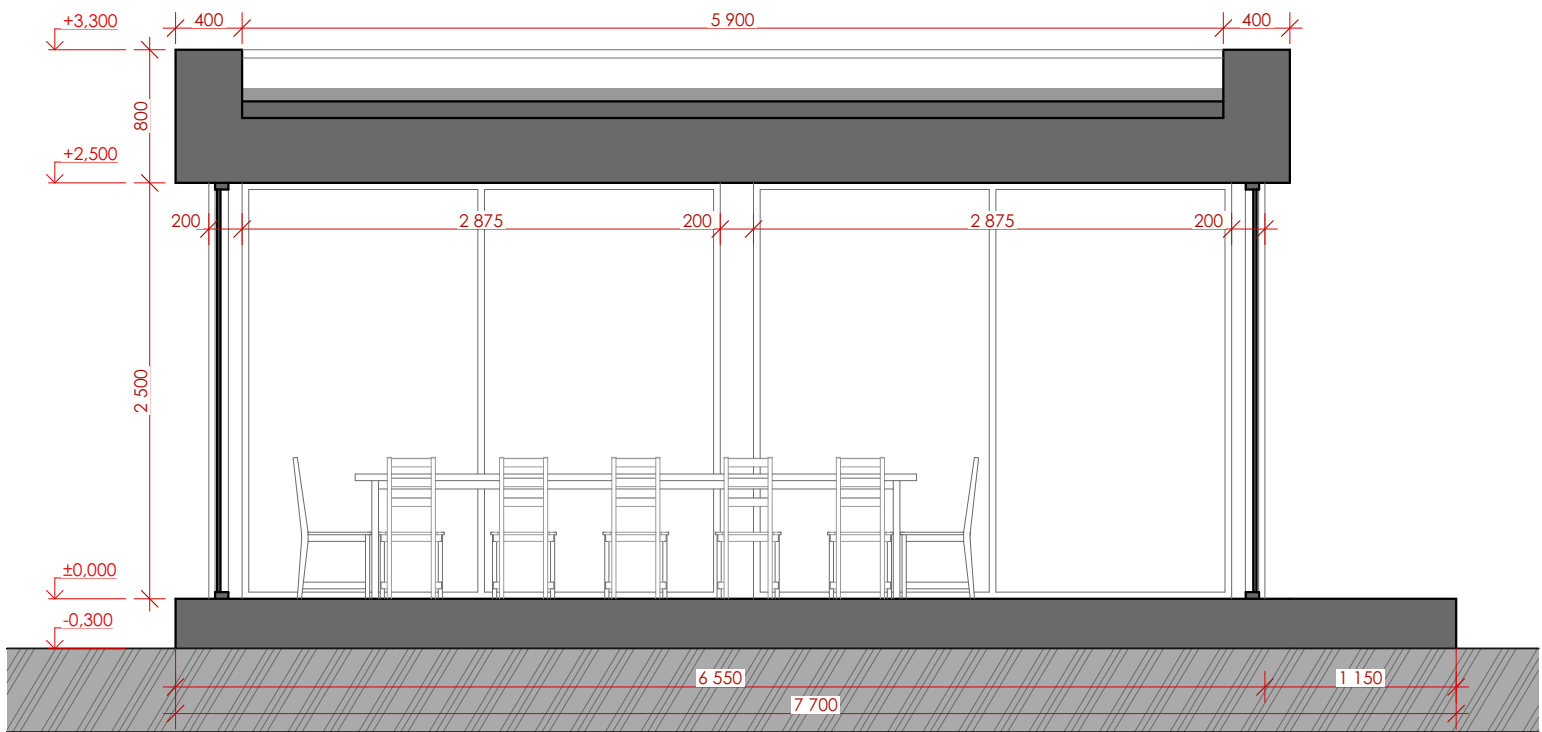

Разрез 4-4

- Примечания:
1. За 0,000 принять уровень пола беседки.
 2. Конструктивные узлы, толщины утеплителя, размеры конструкций определить со специалистами (конструктрами, строителями).
 3. Вент. каналы выполнить герметично и вывести на необходимую высоту предварительно проконсультировавшись со специалистами.
 4. Конструкцию кровли определить со специалистами.
 5. Выполняя отмостку следует предусмотреть минимальный уклон от стен здания.
 6. Предусмотреть ливневую систему водостока.
 7. Размещение, материалы и габариты крылец/порогов определить по месту.
 8. Данные чертежи не носят технический характер и не являются строительными.

						АР - 1			
						Проект архитектурных решений Экопарка «Красивая поляна» в Демском районе г. Уфа РБ на берегу озера Красивая поляна			
Изм.	Кол.уч.	Лист	№Док.	Подп.	Дата		Стадия	Лист	Листов
Разработал	Закиров				04.2025		АР-1	22	
Проверил	Закиров				04.2025	Разрез 3-3, разрез 4-4			
Норм. контроль	Закиров				04.2025				

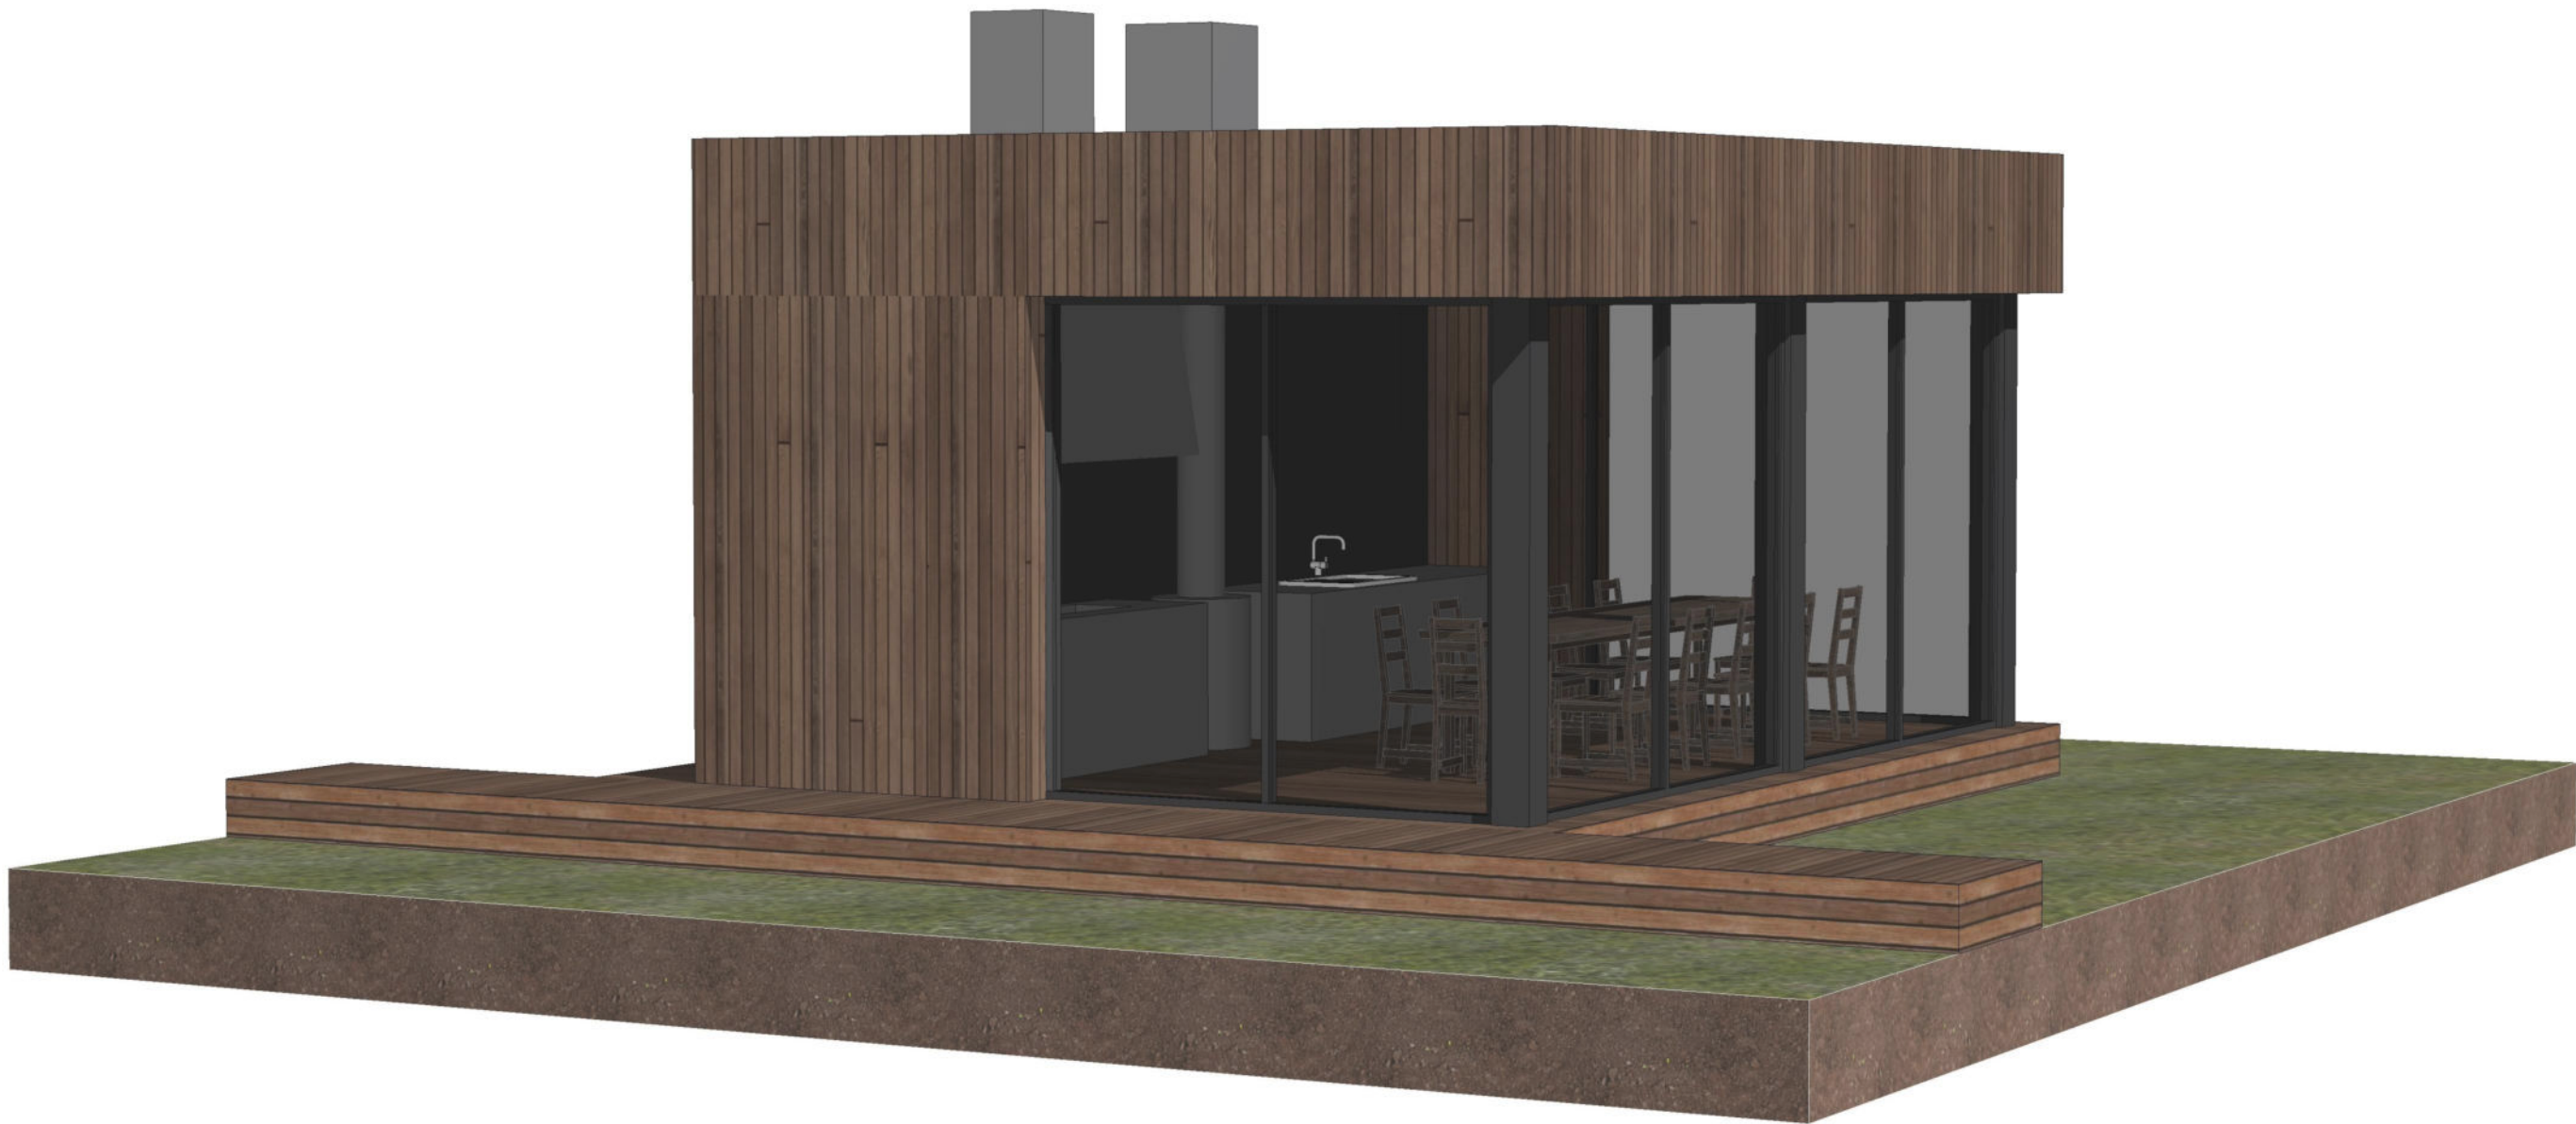


						АР - 1			
						Проект архитектурных решений Экопарка «Красивая поляна» в Демском районе г. Уфа РБ на берегу озера Красивая поляна			
Изм.	Кол.уч.	Лист	№Док.	Подп.	Дата		Стадия	Лист	Листов
Разработал		Закиров			04.2025		АР-1	23	
Проверил		Закиров			04.2025	3D вид беседки			
Норм. контроль		Закиров			04.2025				




						АР - 1			
						Проект архитектурных решений Экопарка «Красивая поляна» в Демском районе г. Уфа РБ на берегу озера Красивая поляна			
Изм.	Кол.уч.	Лист	№Док.	Подп.	Дата		Стадия	Лист	Листов
Разработал		Закиров			04.2025		АР-1	24	
Проверил		Закиров			04.2025	3D вид беседки			
Норм. контроль		Закиров			04.2025				




						АР - 1			
						Проект архитектурных решений Экопарк «Красивая поляна» в Демском районе г. Уфа РБ на берегу озера Красивая поляна			
Изм.	Кол.уч.	Лист	№Док.	Подп.	Дата		Стадия	Лист	Листов
Разработал		Закиров			04.2025		АР-1	25	
Проверил		Закиров			04.2025	3D вид беседки			
Норм. контроль		Закиров			04.2025				

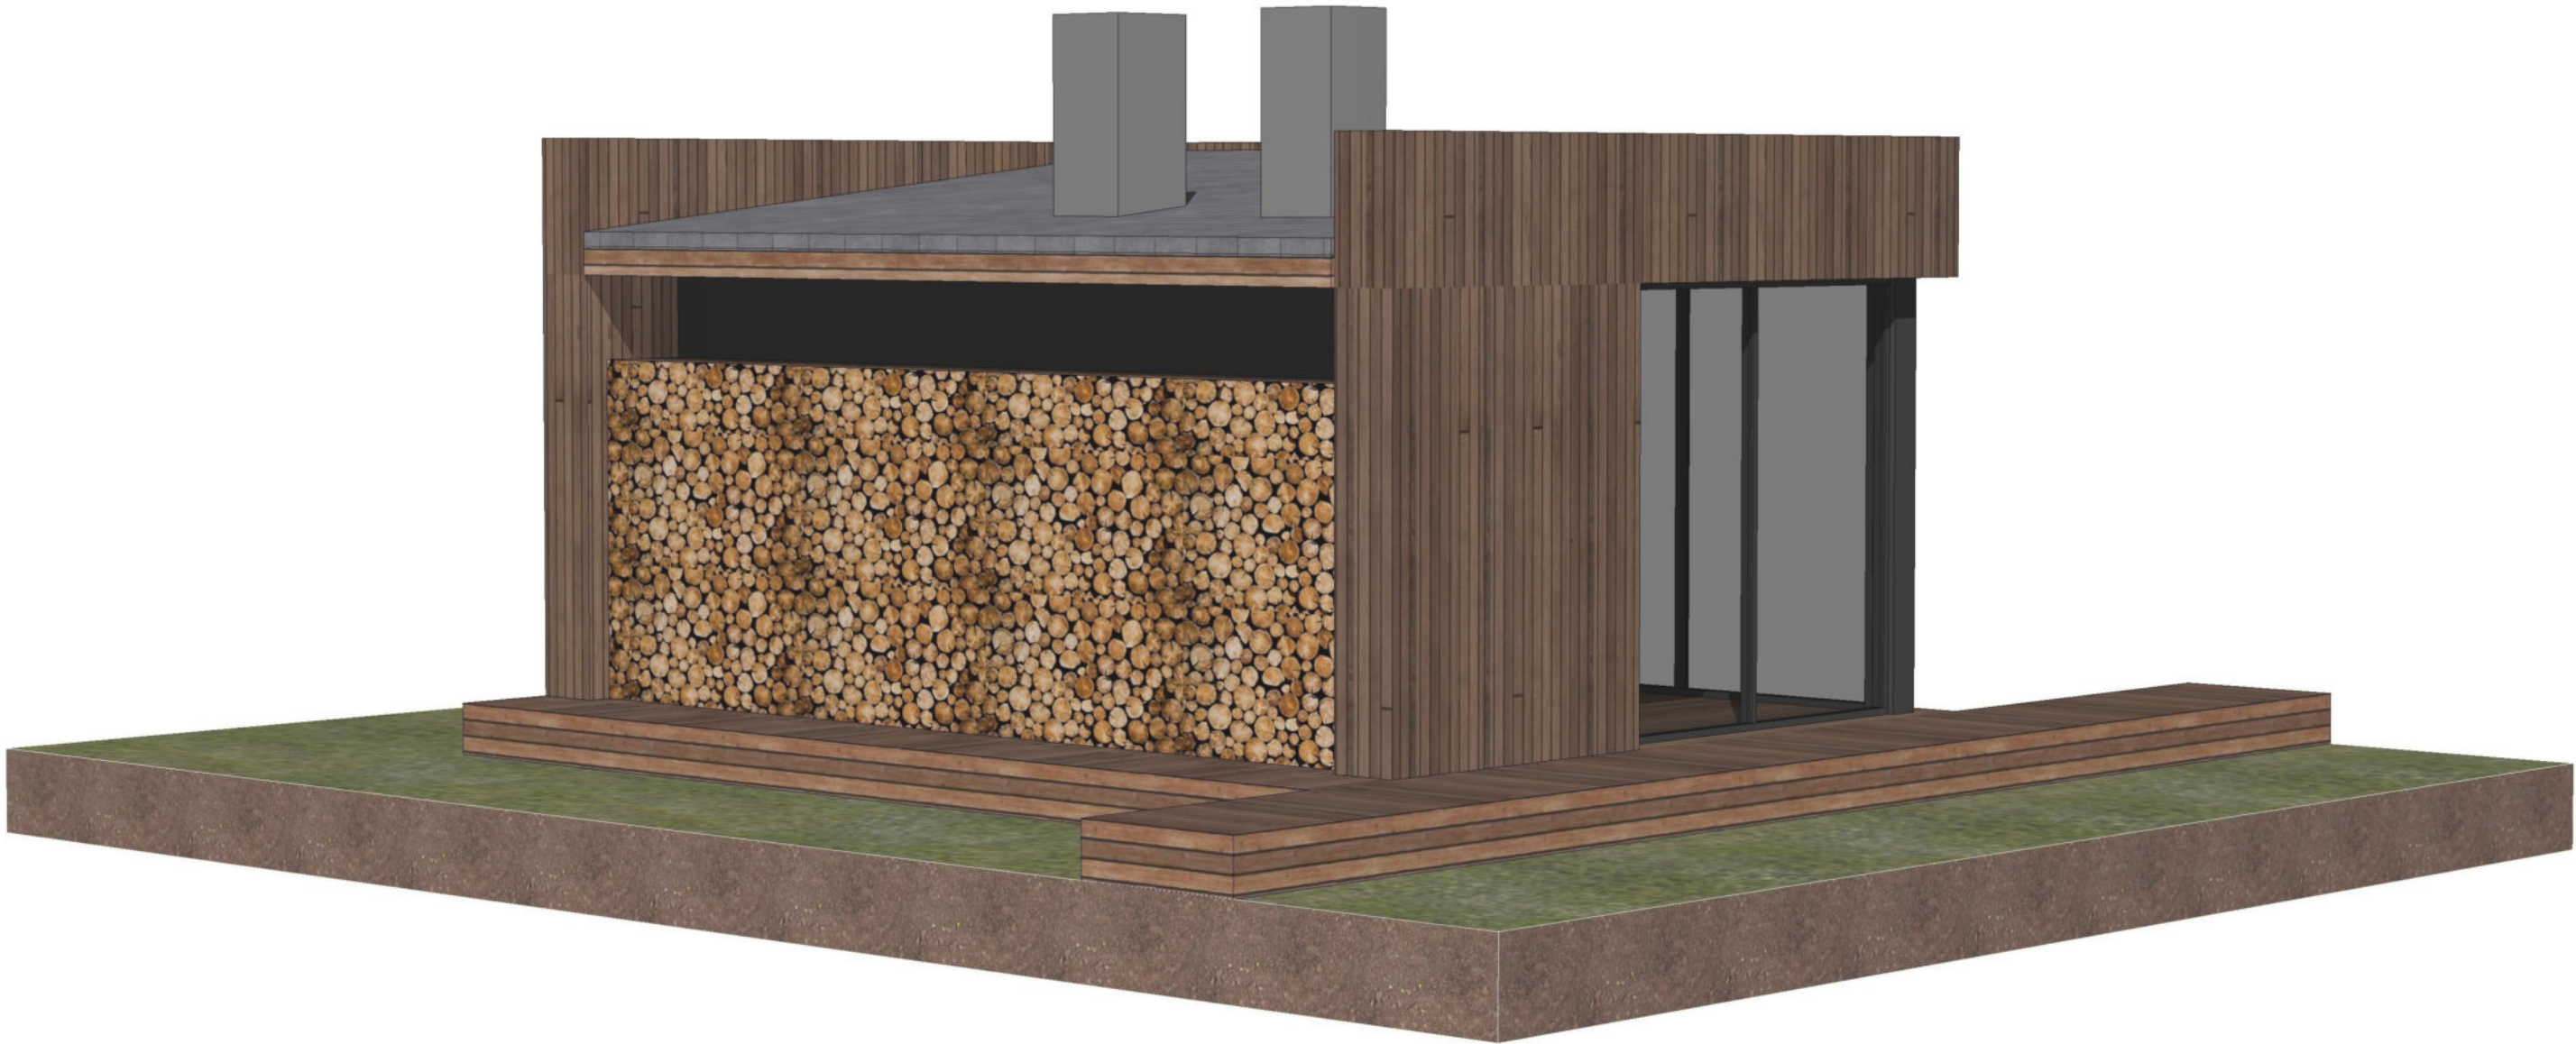

						АР - 1			
						Проект архитектурных решений Экопарка «Красивая поляна» в Демском районе г. Уфа РБ на берегу озера Красивая поляна			
Изм.	Кол.уч.	Лист	№Док.	Подп.	Дата		Стадия	Лист	Листов
Разработал		Закиров			04.2025		АР-1	26	
Проверил		Закиров			04.2025	3D вид беседки			
Норм. контроль		Закиров			04.2025				

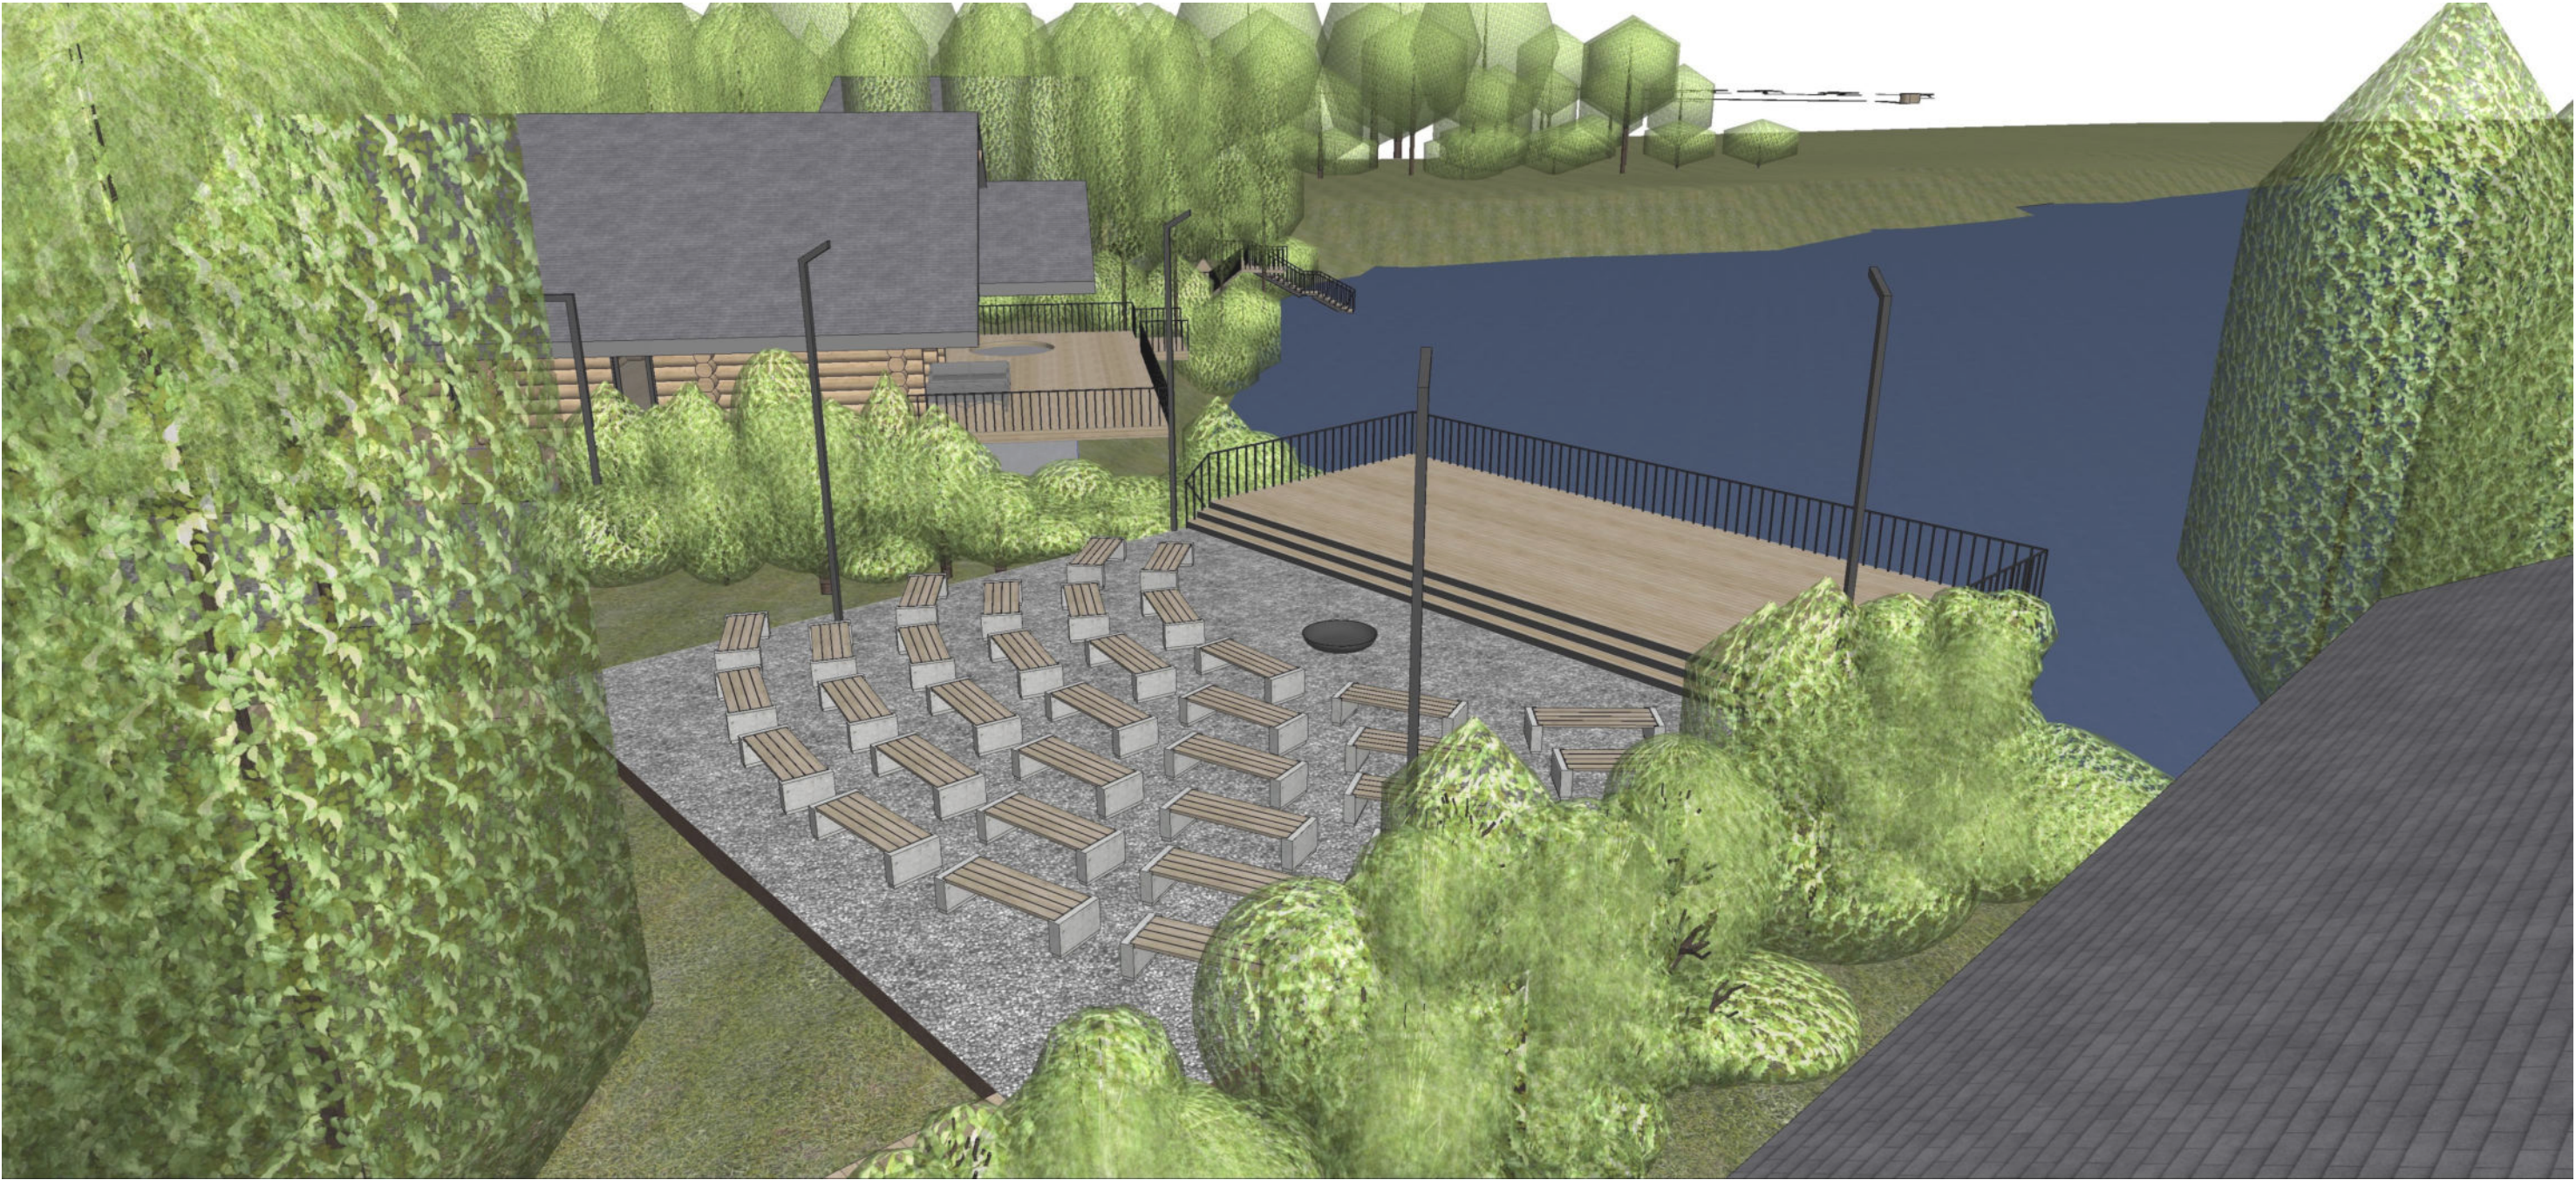


						АР - 1			
						Проект архитектурных решений Экопарка «Красивая поляна» в Демском районе г. Уфа РБ на берегу озера Красивая поляна			
Изм.	Кол.уч.	Лист	№Док.	Подп.	Дата		Стадия	Лист	Листов
Разработал		Закиров			04.2025		АР-1	28	
Проверил		Закиров			04.2025	3D вид лобного места			
Норм. контроль		Закиров			04.2025				


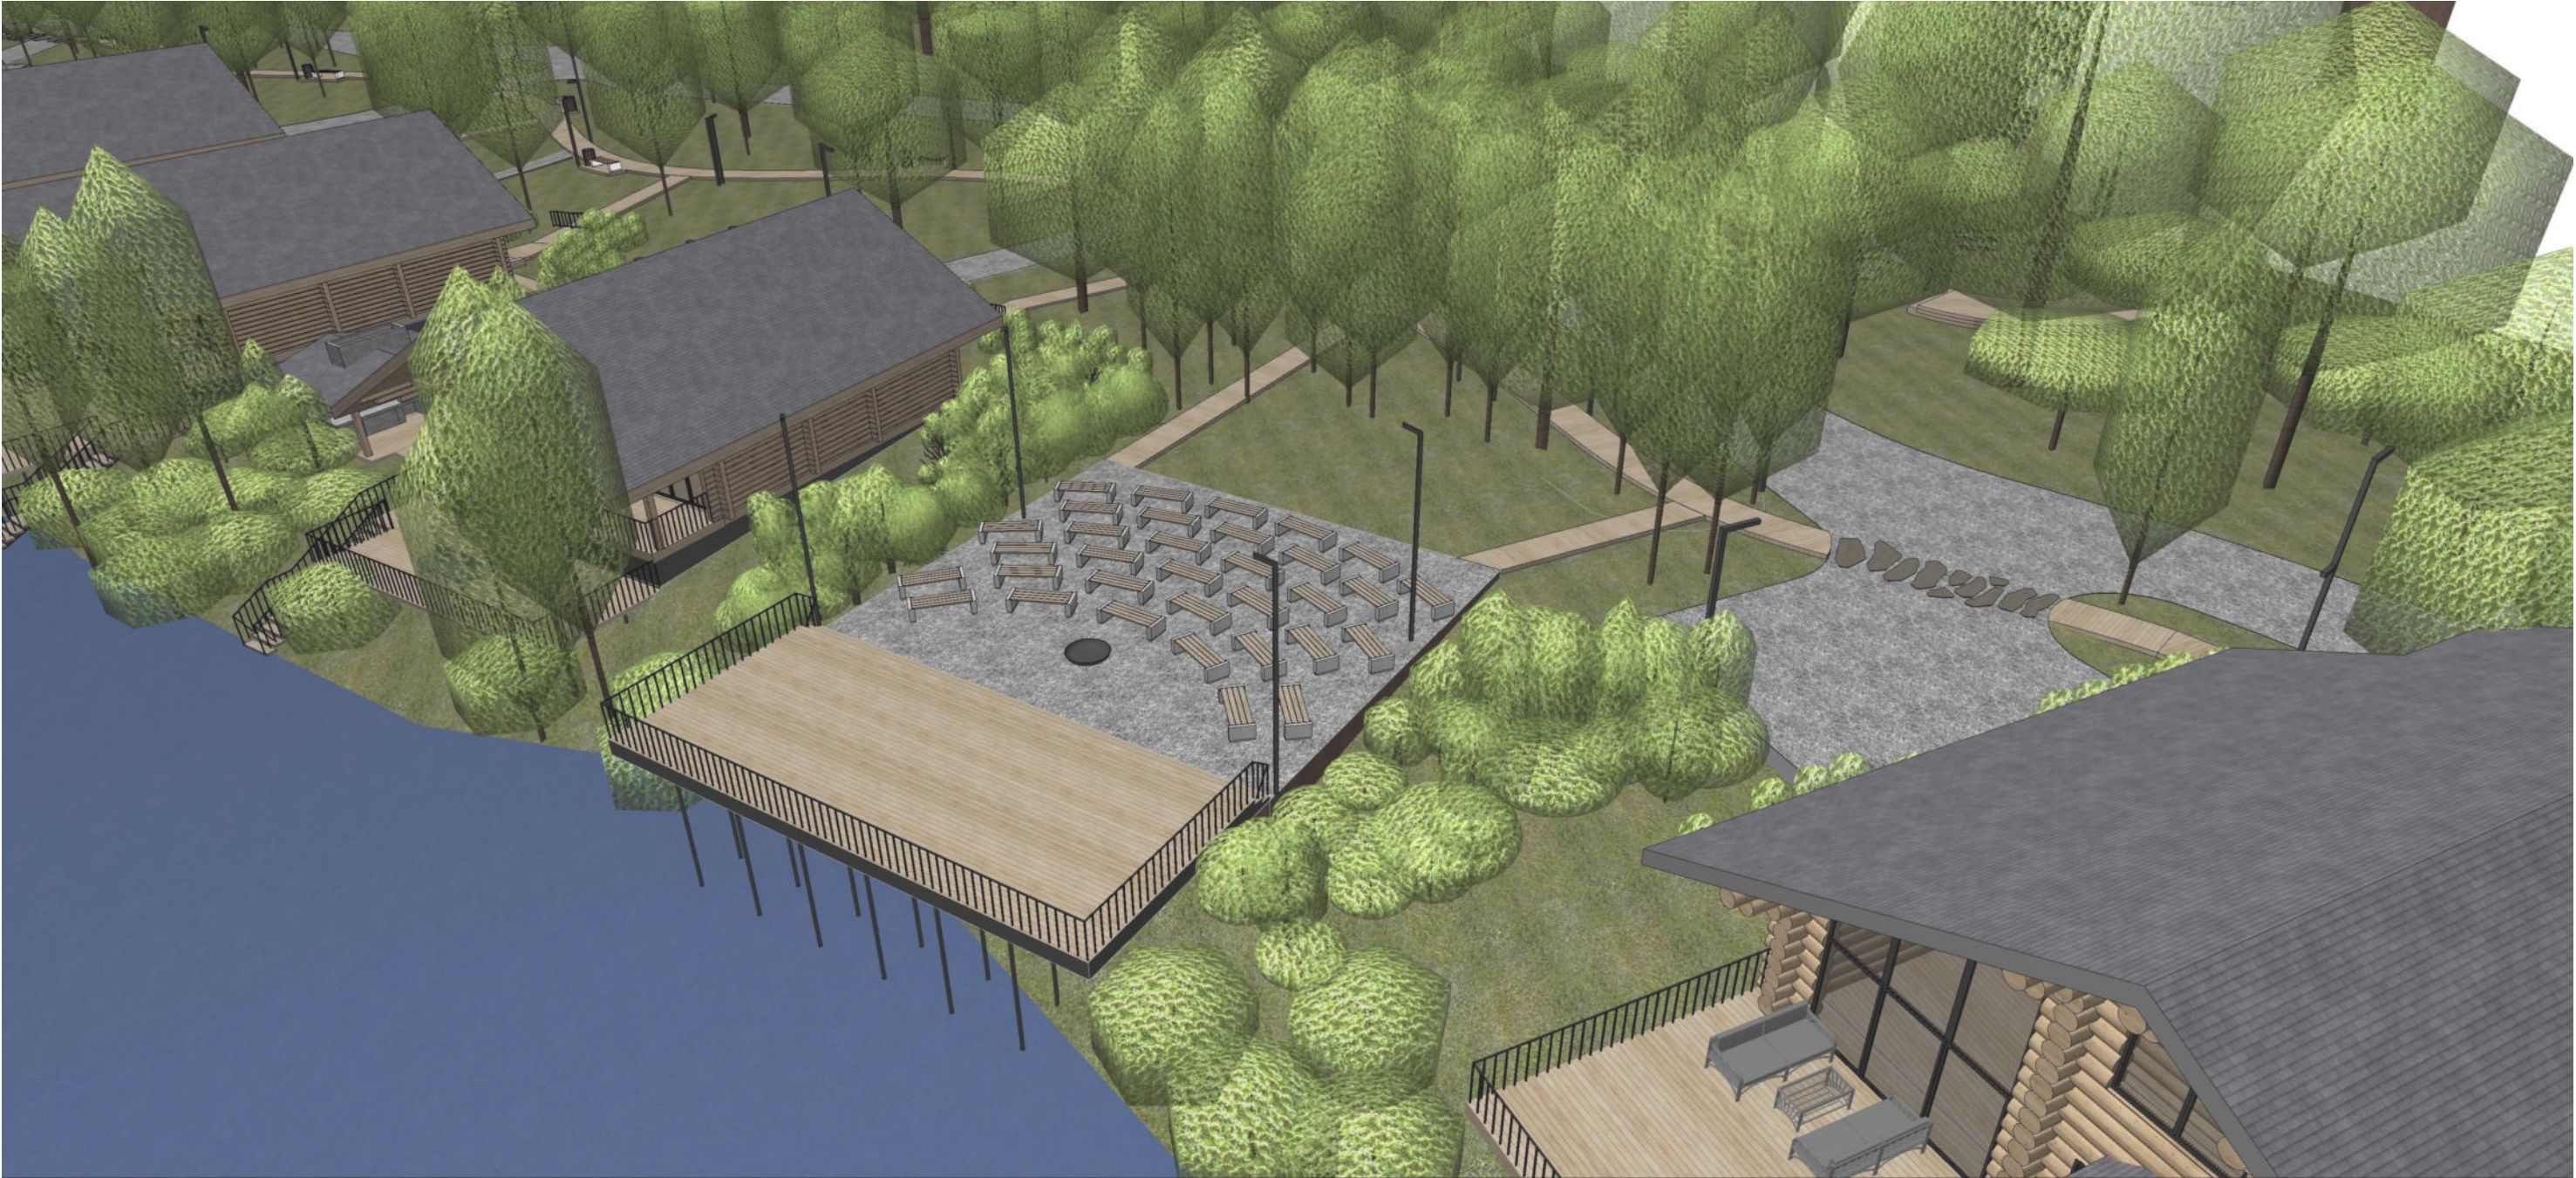


						АР - 1			
						Проект архитектурных решений Экопарк «Красивая поляна» в Демском районе г. Уфа РБ на берегу озера Красивая поляна			
Изм.	Кол.уч.	Лист	№Док.	Подп.	Дата		Стадия	Лист	Листов
Разработал		Закиров			04.2025		АР-1	29	
Проверил		Закиров			04.2025	3D вид лобного места			
Норм. контроль		Закиров			04.2025				


Ведомость наружных материалов ресторана

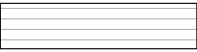Обозначение	Наименование	Площадь	Примечание
	Кровля	271,46 м²	
	Отделка торцов кровли	15,1 м²	
	Отделка фасада	118,1 м²	
	Остекление	128,8 м²	
	Покраска двери	1,68 м²	

Ведомость наружных материалов беседки

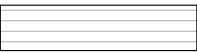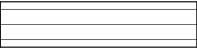Обозначение	Наименование	Площадь	Примечание
	Кровля	28,1 м²	
	Отделка торца кровли	1,5 м²	
	Обшивка деревом	43,41м²	
	Остекление	26,87 м²	
	Покраска труб	4,71 м²	
	Покраска колон	6,00 м²	
	Покраска стены у дровницы	14,75 м²	
	Декинг	11,15 м²	

Ведомость материалов лобной зоны

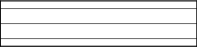Обозначение	Наименование	Площадь	Примечание
	Декинг	93,72 м²	
	Гравий/щебень	177,5 м²	

Примечания:
1. Количество материала указано без запаса.

						АР - 1				
						Проект архитектурных решений Экопарка «Красивая поляна» в Демском районе г. Уфа РБ на берегу озера Красивая поляна				
Изм.	Кол.уч.	Лист	№Док.	Подп.	Дата			Стадия	Лист	Листов
Разработал		Закиров			04.2025			АР-1	30	
Проверил		Закиров			04.2025	Спецификация				
Норм. контроль		Закиров			04.2025					